



Republika e Kosovës

Qeveria - Vlada



Ministria e Mjedisit dhe Planifikimit Hapësinor / Ministerstvo Sredine i Prstrng Planiranja
AGJENCIJA KADASTRALE E KOSOVËS / KATASTARSKA AGENCIJA KOSOVA

Situacioni i terrenit

Zyra kadastrale kmunale / pëtinska katastarska kancelaria: Ferizaj

Zona kadastrale / Katastarska zona: Ferizaj

Nr. i njësisë kadastrale / Br. katastarske jedinice : 2602-0


Numri i lëndës / Broj predmeta:

Shkalla e zvoglimit / Razmerra plana 1: 200

Lista e koordinatave të pikave të matura:

| Nr | Y | X | H | DSC |
|----|-------------|-------------|---------|----------------|
| 88 | 751319.293 | 469109.276 | 619.928 | FS1 |
| 92 | 751314.444 | 4691697.230 | 619.819 | FS2 |
| 53 | 751311.118 | 4691717.922 | 634.439 | KULMI |
| 17 | 7513126.261 | 4691714.600 | 620.056 | KYQYE-USIELLES |
| 1 | 7513135.568 | 4691722.874 | 620.112 | PERDHESA |
| 2 | 7513132.501 | 4691720.099 | 620.112 | PERDHESA |
| 6 | 7513133.257 | 4691719.323 | 620.112 | PERDHESA |
| 7 | 7513128.986 | 4691715.505 | 620.112 | PERDHESA |
| 11 | 7513130.596 | 4691713.706 | 620.112 | PERDHESA |
| 12 | 7513129.454 | 4691712.656 | 620.112 | PERDHESA |
| 13 | 7513129.172 | 4691712.005 | 620.112 | PERDHESA |
| 14 | 7513129.620 | 4691710.995 | 620.112 | PERDHESA |
| 15 | 7513132.685 | 4691707.655 | 620.112 | PERDHESA |
| 65 | 7513134.155 | 4691707.022 | 620.112 | PERDHESA |
| 67 | 7513135.857 | 4691707.745 | 620.112 | PERDHESA |
| 68 | 7513143.253 | 4691714.464 | 620.112 | PERDHESA |
| 21 | 7513131.355 | 4691697.861 | 619.721 | PUSET-FEKAL |

| Nr | Y | X | H | DSC |
|----|-------------|-------------|---------|------------------|
| 8 | 7513128.764 | 4691715.831 | 620.112 | SHKALET |
| 9 | 7513126.840 | 4691714.119 | 620.112 | SHKALET |
| 10 | 7513129.231 | 4691711.487 | 620.112 | SHKALET |
| 22 | 7513130.176 | 4691693.961 | 619.757 | SHTYLL-ELEKTRIKE |
| 86 | 7513106.321 | 4691683.375 | 619.497 | S1 |
| 87 | 7513162.150 | 4691668.332 | 619.825 | S12 |
| 54 | 7513135.505 | 4691723.319 | 631.507 | STREHA |
| 55 | 7513132.018 | 4691720.161 | 631.507 | STREHA |
| 56 | 7513133.002 | 4691719.123 | 631.507 | STREHA |
| 57 | 7513132.790 | 4691719.412 | 631.507 | STREHA |
| 58 | 7513129.105 | 4691716.044 | 631.507 | STREHA |
| 59 | 7513127.020 | 4691714.199 | 631.507 | STREHA |
| 60 | 7513127.147 | 4691713.062 | 631.507 | STREHA |
| 61 | 7513127.359 | 4691711.499 | 631.507 | STREHA |
| 62 | 7513131.843 | 4691706.582 | 631.507 | STREHA |
| 63 | 7513133.047 | 4691705.902 | 631.507 | STREHA |
| 64 | 7513133.876 | 4691705.829 | 631.507 | STREHA |
| 84 | 7513136.690 | 4691707.949 | 631.507 | STREHA |
| 85 | 7513143.745 | 4691714.446 | 631.507 | STREHA |

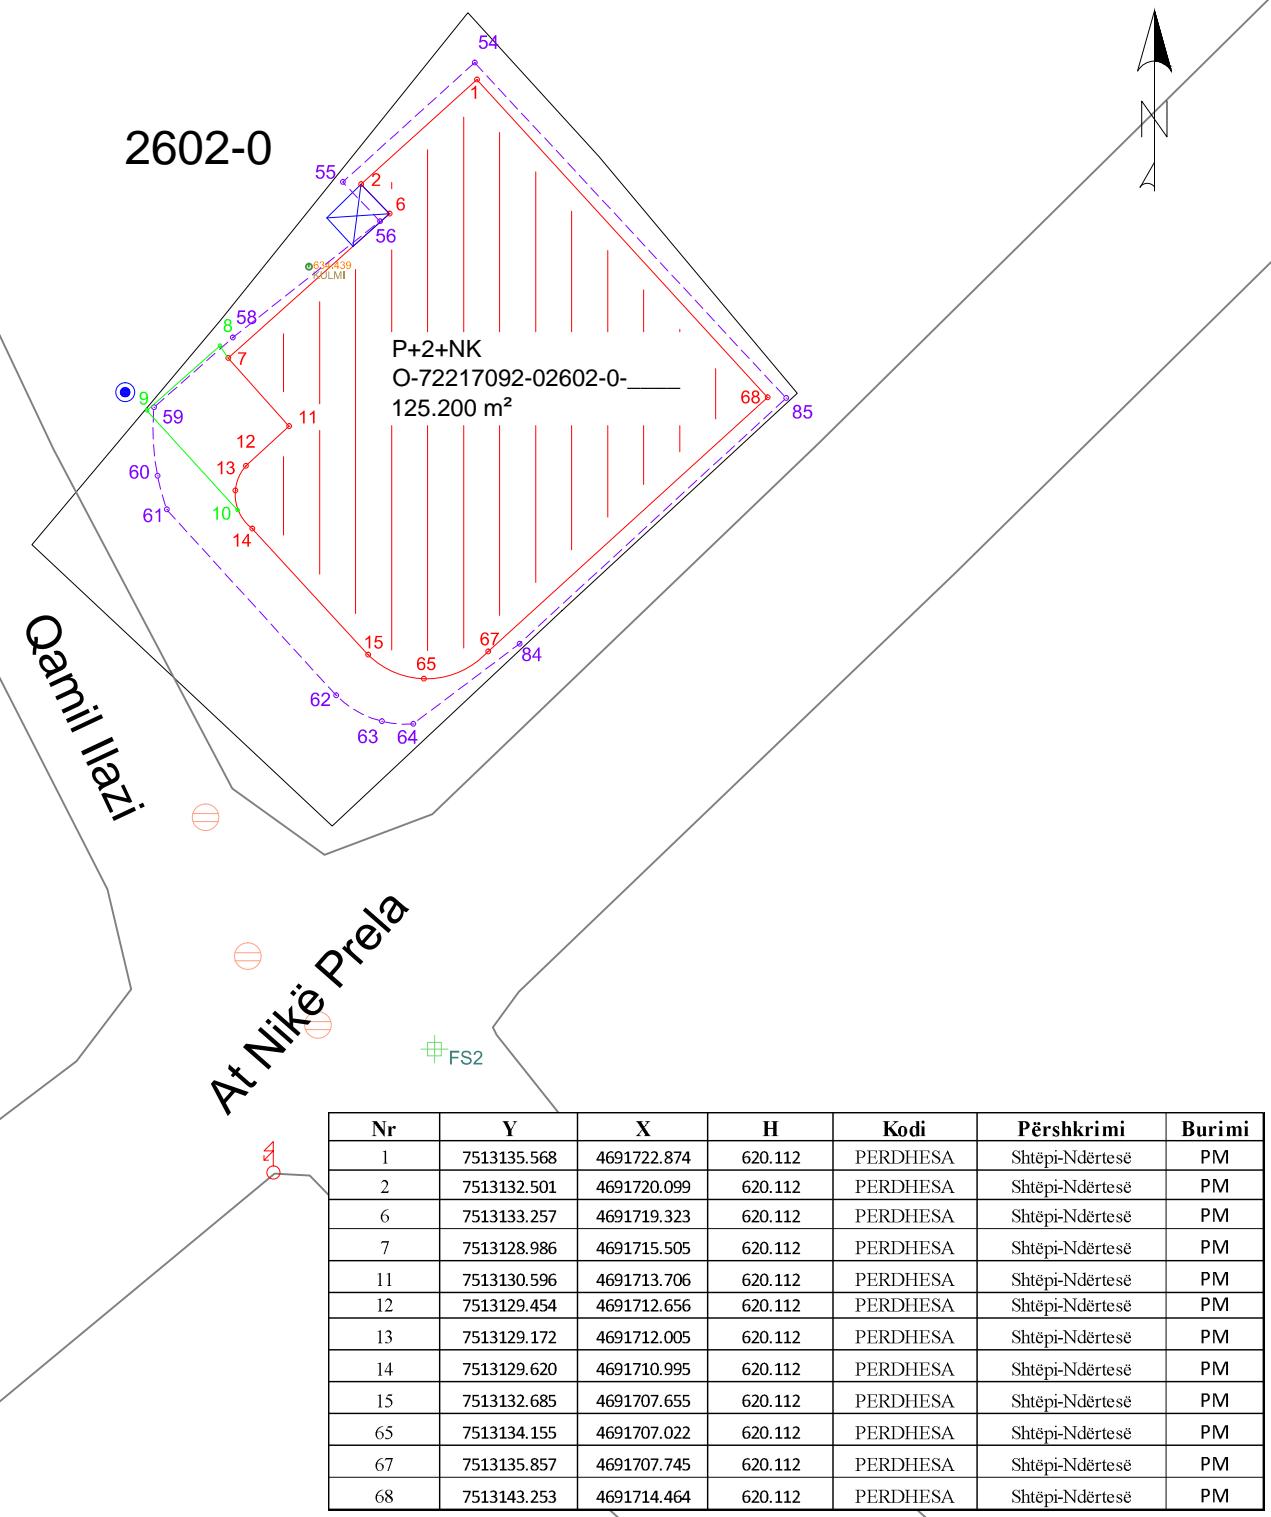

Shpjegues:

- 91 Pikë e objekteve fqinje
- Rr. Emri i rrugës
- P4 Ndërtesa në trajtim për legalizim
- Ndërtesa tjera
- Aneks Ndërtimi
- Shtyllë elektrike
- Puset e ujësjellësít
- Puset e ujërave të zeza
- Pikë e murit
- Pikë e kulmit
- Bunari

Rilevoi / Snimi: LIRIDON SEJDIU

(emri dhe mbiemri i gjedjetit/kompanisë/ ime i prezime gedeta/ kompanije)

Nr. i licencës / Br. licence: 140

Data e rilevimit / Datum snimanja: 12.04.2021

Nënshkrimi / Potpis: v.v.



Republika e Kosovës

Qeveria - Vlada



Ministria e Mjedisit dhe Planifikimit Hapësinor / Ministerstvo Sredine i Prstrng Planiranja
AGJENCIJA KADASTRALE E KOSOVËS / KATASTARSKA AGENCIJA KOSOVA

Situacioni i terrenit

Orto 2004

Ferizaj

Zona kadastrale / Katastarska zona: Ferizaj

Nr. i njësisë kadastrale / Br. katastarske jedinice : 2602-0

Numri i lëndës / Broj predmeta:

Shkalla e zvoglimit / Razmera plana 1: 200

Lista e koordinatave të pikave të matura:

| Nr | Y | X | H | DSC |
|----|-------------|-------------|---------|---------------|
| 88 | 751319.293 | 469109.276 | 619.928 | FS1 |
| 92 | 751314.444 | 4691697.230 | 619.819 | FS2 |
| 53 | 7513131.118 | 4691717.922 | 634.439 | KULMI |
| 17 | 7513126.261 | 4691714.600 | 620.056 | KYQE-USIELLES |
| 1 | 7513135.568 | 4691722.874 | 620.112 | PERDHESA |
| 2 | 7513132.501 | 4691720.099 | 620.112 | PERDHESA |
| 6 | 7513133.257 | 4691719.323 | 620.112 | PERDHESA |
| 7 | 7513128.986 | 4691715.505 | 620.112 | PERDHESA |
| 11 | 7513130.596 | 4691713.706 | 620.112 | PERDHESA |
| 12 | 7513129.454 | 4691712.656 | 620.112 | PERDHESA |
| 13 | 7513129.172 | 4691712.005 | 620.112 | PERDHESA |
| 14 | 7513129.620 | 4691710.995 | 620.112 | PERDHESA |
| 15 | 7513132.685 | 4691707.655 | 620.112 | PERDHESA |
| 65 | 7513134.155 | 4691707.022 | 620.112 | PERDHESA |
| 67 | 7513135.857 | 4691707.745 | 620.112 | PERDHESA |
| 68 | 7513143.253 | 4691714.464 | 620.112 | PERDHESA |
| 21 | 7513131.355 | 4691697.861 | 619.721 | PUSET-FEKAL |

| Nr | Y | X | H | DSC |
|----|-------------|-------------|---------|------------------|
| 8 | 7513128.764 | 4691715.831 | 620.112 | SHKALET |
| 9 | 7513126.840 | 4691714.119 | 620.112 | SHKALET |
| 10 | 7513129.231 | 4691711.487 | 620.112 | SHKALET |
| 22 | 7513130.176 | 4691693.961 | 619.757 | SHTYLL-ELEKTRIKE |
| 86 | 7513106.321 | 4691683.375 | 619.497 | S1 |
| 87 | 7513162.150 | 4691668.332 | 619.825 | S12 |
| 54 | 7513135.505 | 4691723.319 | 631.507 | STREHA |
| 55 | 7513132.018 | 4691720.161 | 631.507 | STREHA |
| 56 | 7513133.002 | 4691719.123 | 631.507 | STREHA |
| 57 | 7513132.790 | 4691719.412 | 631.507 | STREHA |
| 58 | 7513129.105 | 4691716.044 | 631.507 | STREHA |
| 59 | 7513127.020 | 4691714.199 | 631.507 | STREHA |
| 60 | 7513127.147 | 4691713.062 | 631.507 | STREHA |
| 61 | 7513127.359 | 4691711.499 | 631.507 | STREHA |
| 62 | 7513131.843 | 4691706.582 | 631.507 | STREHA |
| 63 | 7513133.047 | 4691705.902 | 631.507 | STREHA |
| 64 | 7513133.876 | 4691705.829 | 631.507 | STREHA |
| 84 | 7513136.690 | 4691710.949 | 631.507 | STREHA |
| 85 | 7513143.745 | 4691714.446 | 631.507 | STREHA |

Shpjegues:


- 91 Pikë e objekteve fqinje
- Rr. Emri i rrugës
- +P4 Pikë e rrjetës gjeodezike
- 131 Pikë e strehëve
- 81 Pikë e terasës
- 10 Pikë e objektit
- 93 Pikë e murit
- 92 Pikë e kulmit
- Strehët
- Shkallët
- Bunari

Rilevoi / Snimi: LIRIDON SEJDIU
(emri dhe mbiemri i gjedjetit/kompanisë/ imë i prezime gedeta/ kompanije)

Nr. i licencës / Br. licence: 140

Data e rilevimit / Datum snimanja: 12.04.2021

Nënshkrimi / Potpis: v.v.

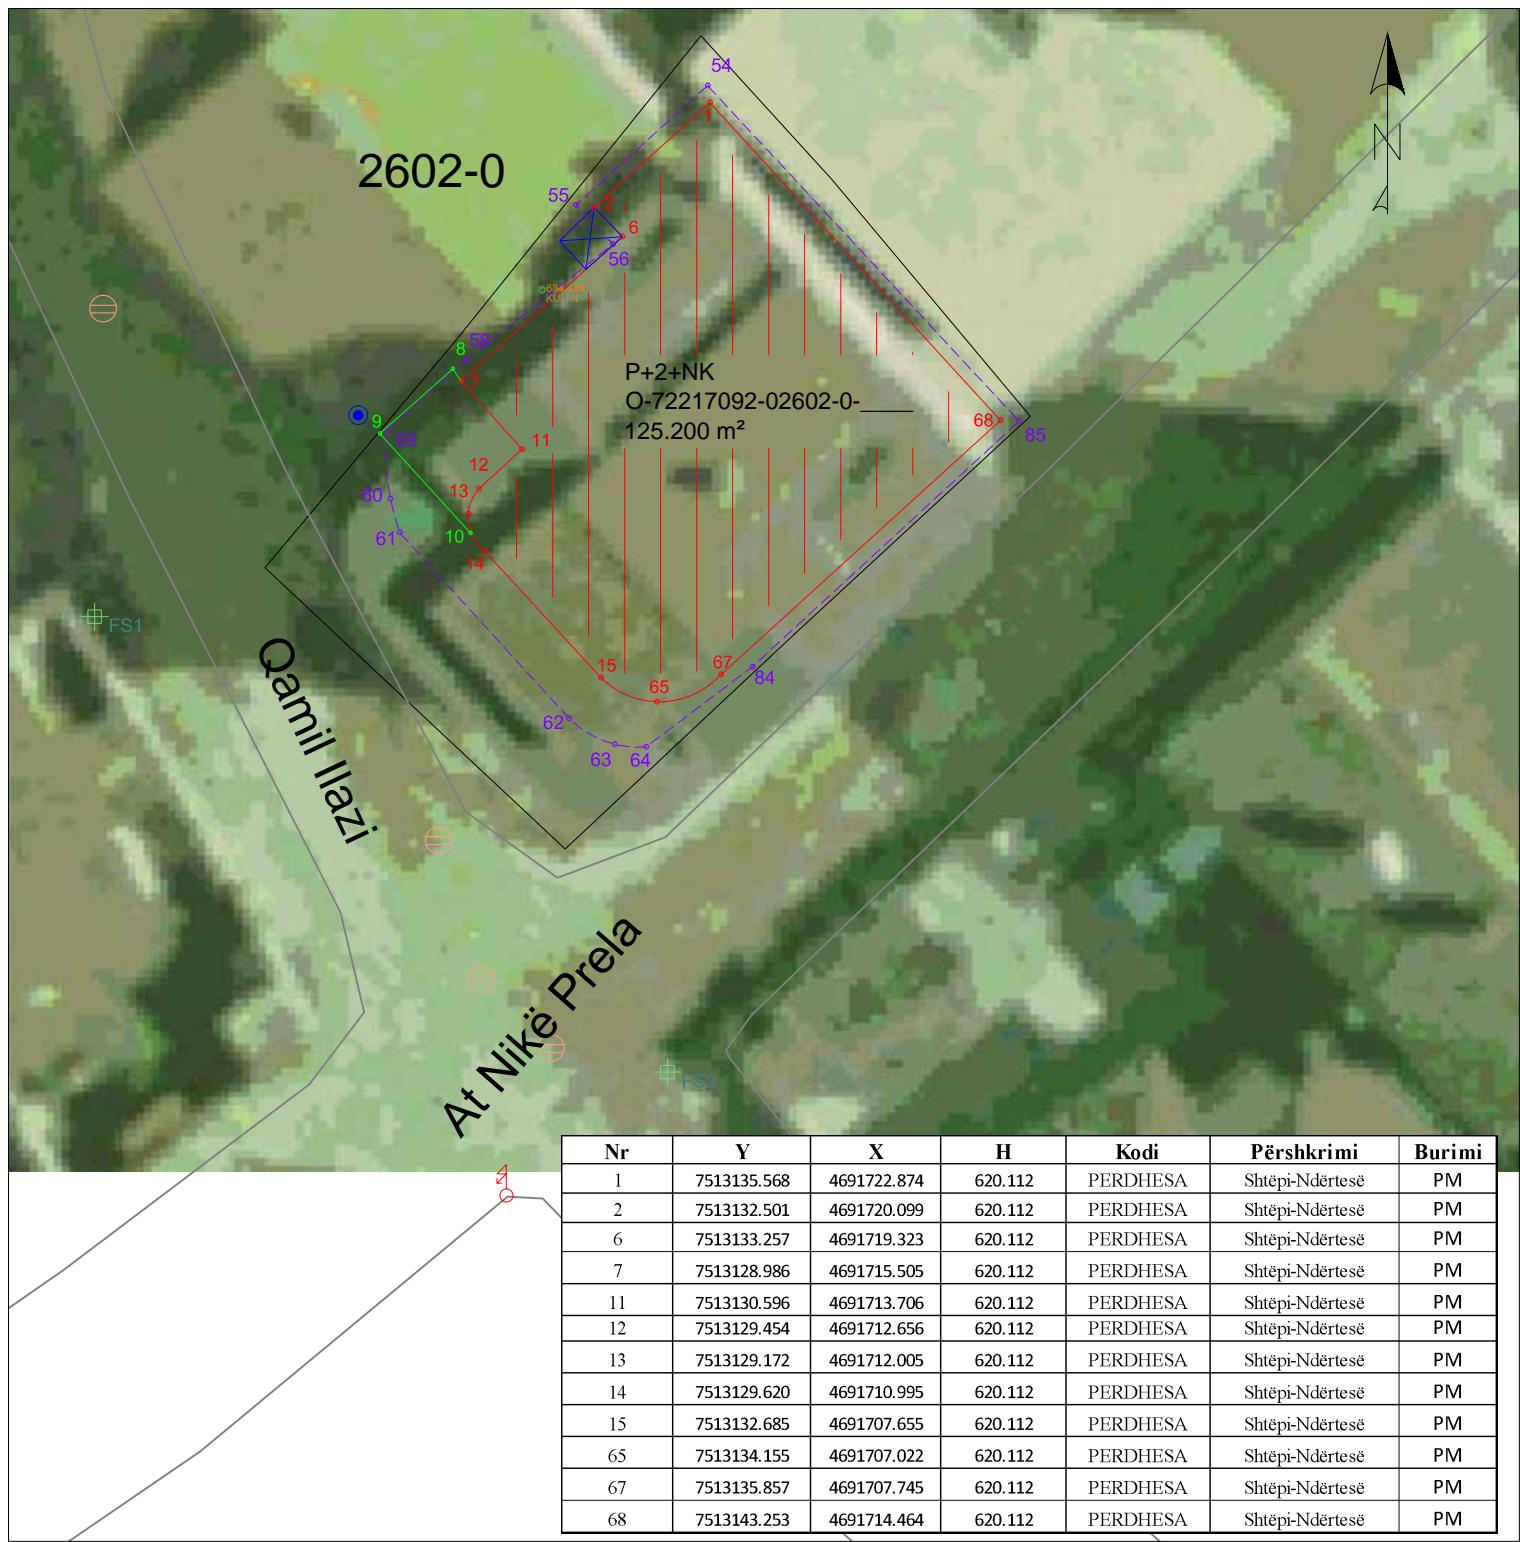



Republika e Kosovës

Qeveria - Vlada

Ministria e Mjedisit dhe Planifikimit Hapësinor / Ministerstvo Sredine i Prstrng Planiranja
AGJENCIA KADASTRALE E KOSOVËS / KATASTARSKA AGENCIJA KOSOVA

Situacioni i terrenit

Orto 2018

Ferizaj

Zyra kadastrale kmunale / pëtinska katastarska kancelaria: _____

Ferizaj

Nr. i njësisë kadastrale / Br. katastarske jedinice : _____

2602-0

Numri i lëndës / Broj predmeta: _____

Shkalla e zvoglimit / Razmerra plana 1: _____

200

Lista e koordinatave të pikave të matura:

| Nr | Y | X | H | DSC |
|----|-------------|-------------|---------|----------------|
| 88 | 751319.293 | 469109.276 | 619.928 | FS1 |
| 92 | 751314.444 | 4691697.230 | 619.819 | FS2 |
| 53 | 7513131.118 | 4691717.922 | 634.439 | KULMI |
| 17 | 7513126.261 | 4691714.600 | 620.056 | KYQJE-USIELLES |
| 1 | 7513135.568 | 4691722.874 | 620.112 | PERDHESA |
| 2 | 7513132.501 | 4691720.099 | 620.112 | PERDHESA |
| 6 | 7513133.257 | 4691719.323 | 620.112 | PERDHESA |
| 7 | 7513128.986 | 4691715.505 | 620.112 | PERDHESA |
| 11 | 7513130.596 | 4691713.706 | 620.112 | PERDHESA |
| 12 | 7513129.454 | 4691712.656 | 620.112 | PERDHESA |
| 13 | 7513129.172 | 4691712.005 | 620.112 | PERDHESA |
| 14 | 7513129.620 | 4691710.995 | 620.112 | PERDHESA |
| 15 | 7513132.685 | 4691707.655 | 620.112 | PERDHESA |
| 65 | 7513134.155 | 4691707.022 | 620.112 | PERDHESA |
| 67 | 7513135.857 | 4691707.745 | 620.112 | PERDHESA |
| 68 | 7513143.253 | 4691714.464 | 620.112 | PERDHESA |
| 21 | 7513131.355 | 4691697.861 | 619.721 | PUSET-FEKAL |

| Nr | Y | X | H | DSC |
|----|-------------|-------------|---------|------------------|
| 8 | 7513128.764 | 4691715.831 | 620.112 | SHKALET |
| 9 | 7513126.840 | 4691714.119 | 620.112 | SHKALET |
| 10 | 7513129.231 | 4691711.487 | 620.112 | SHKALET |
| 22 | 7513130.176 | 4691693.961 | 619.757 | SHTYLL-ELEKTRIKE |
| 86 | 7513106.321 | 4691683.375 | 619.497 | ST1 |
| 87 | 7513162.150 | 4691668.332 | 619.825 | ST2 |
| 54 | 7513135.505 | 4691723.319 | 631.507 | STREHA |
| 55 | 7513132.018 | 4691720.161 | 631.507 | STREHA |
| 56 | 7513133.002 | 4691719.123 | 631.507 | STREHA |
| 57 | 7513132.790 | 4691719.412 | 631.507 | STREHA |
| 58 | 7513129.105 | 4691716.044 | 631.507 | STREHA |
| 59 | 7513127.020 | 4691714.199 | 631.507 | STREHA |
| 60 | 7513127.147 | 4691713.062 | 631.507 | STREHA |
| 61 | 7513127.359 | 4691711.499 | 631.507 | STREHA |
| 62 | 7513131.843 | 4691706.582 | 631.507 | STREHA |
| 63 | 7513133.047 | 4691705.902 | 631.507 | STREHA |
| 64 | 7513133.876 | 4691705.829 | 631.507 | STREHA |
| 84 | 7513136.690 | 4691707.949 | 631.507 | STREHA |
| 85 | 7513143.745 | 4691714.446 | 631.507 | STREHA |



Shpjegues:

- 91 Kufi kadastral (nga SIKTK-G)
- Rr. Emri i rrugës
- P4 Plikë e rrjetës gjeodezike
- 131 Pikë e strehëve
- 81 Pikë e terasës
- 10 Pikë e objektit
- 93 Pikë e murit
- 92 Pikë e kulmit
- Strehët
- Shkallët
- Bunari

Rilevoi / Snimi: **LIRIDON SEJDIU**

(emri dhe mbiemri i gjedjetit/kompanisë/ ime i prezime gedeta/ kompanije)

Nr. i licencës / Br. licence: **140**

Data e rilevimit / Datum snimanja: **12.04.2021**

Nënshkrimi / Potpis: _____
v.v.



Republika e Kosovës
Republika Kosova-Republic of Kosovo
Qeveria e Kosovës- Vlada Kosova- Government of Kosovo
Ministria e Infrastrukturës dhe Ambientit/ Ministrastvo Infrastrukture i Sredine/ Ministry of Infrastructure and Environment
AGJENCIA KADASTRALE E KOSOVËS/KOSOVSKA KATASTARSKA AGENCIJA/ KOSOVO CADASTRAL AGENCY

Komuna: Ferizaj


Numri i njësis kadastrale: 02602-0

Zona Kadastrale: Ferizaj

Sistemi koordinat: KosovaRef01

| Nr | Y | X | H | Kodi | Përshkrimi | Burimi |
|----|-------------|-------------|---------|----------|-----------------|--------|
| 1 | 7513135.568 | 4691722.874 | 620.112 | PERDHESA | Shtëpi-Ndërtesë | PM |
| 2 | 7513132.501 | 4691720.099 | 620.112 | PERDHESA | Shtëpi-Ndërtesë | PM |
| 6 | 7513133.257 | 4691719.323 | 620.112 | PERDHESA | Shtëpi-Ndërtesë | PM |
| 7 | 7513128.986 | 4691715.505 | 620.112 | PERDHESA | Shtëpi-Ndërtesë | PM |
| 11 | 7513130.596 | 4691713.706 | 620.112 | PERDHESA | Shtëpi-Ndërtesë | PM |
| 12 | 7513129.454 | 4691712.656 | 620.112 | PERDHESA | Shtëpi-Ndërtesë | PM |
| 13 | 7513129.172 | 4691712.005 | 620.112 | PERDHESA | Shtëpi-Ndërtesë | PM |
| 14 | 7513129.620 | 4691710.995 | 620.112 | PERDHESA | Shtëpi-Ndërtesë | PM |
| 15 | 7513132.685 | 4691707.655 | 620.112 | PERDHESA | Shtëpi-Ndërtesë | PM |
| 65 | 7513134.155 | 4691707.022 | 620.112 | PERDHESA | Shtëpi-Ndërtesë | PM |
| 67 | 7513135.857 | 4691707.745 | 620.112 | PERDHESA | Shtëpi-Ndërtesë | PM |
| 68 | 7513143.253 | 4691714.464 | 620.112 | PERDHESA | Shtëpi-Ndërtesë | PM |

| | | | |
|---|----------------|----------------------|--|
| Gjeodeti / Kompania gjeodete e licencuar: | Liridon Sejdiu | Nënshkrimi dhe vula: | |
| Numri i licencës | 140 | | |

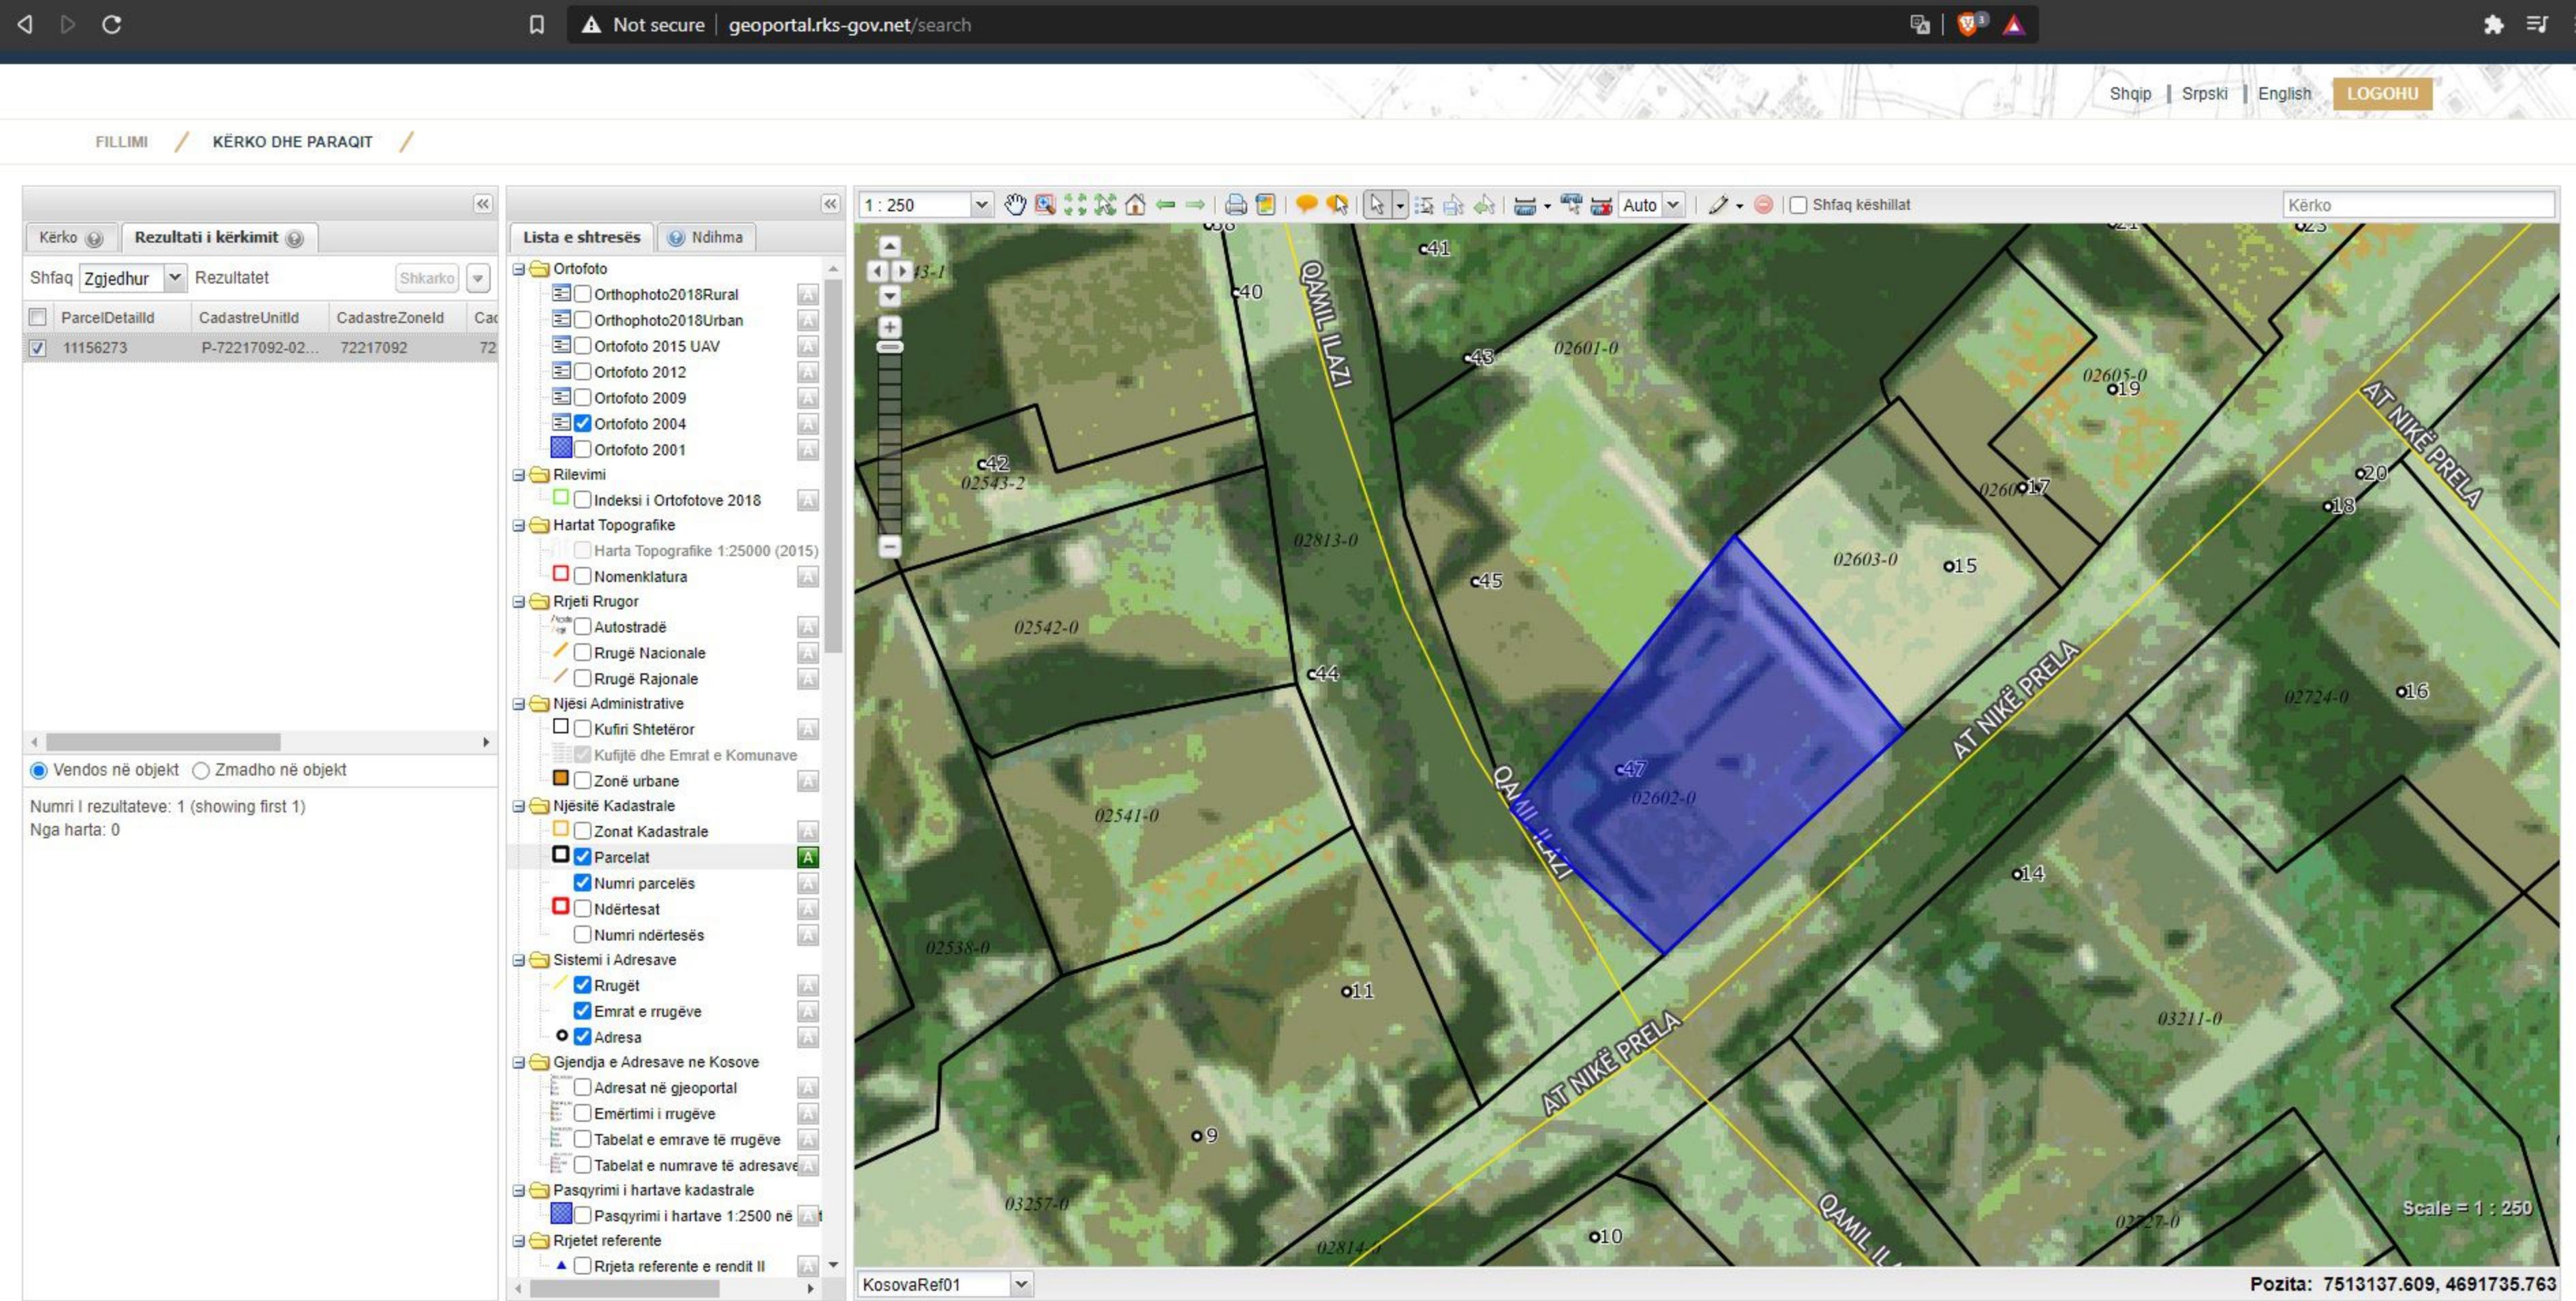


Zyra kadastrale komunale / Opštinska katastarska kancelarija: FerizajNr. i njësisë kadastrale / Br. katastarske jedinice : 2602-0Zona kadastrale / Katastarska zona: Ferizaj

Numri i lëndës / Broj predmeta: _____

Lloji i njësisë kadastrale / Vrsta katastarske jedinice : NdërtesëShkalla e zvoglimit / Razmera plana 1: 200**Republika e Kosovës****Republika Kosova-Republic of Kosovo****Qeveria -Vlada-Government****Ministria e Mjedisit dhe Planifikimit Hapësinor /Ministarstvo Sredine i Prostornog Planiranja/Ministry of Environment and Spatial Planning**

AGJENCIA KADASTRALE E KOSOVËS/KATASTARSKA AGECIJA KOSOVA/KOSOVA CADASTRAL AGENCY

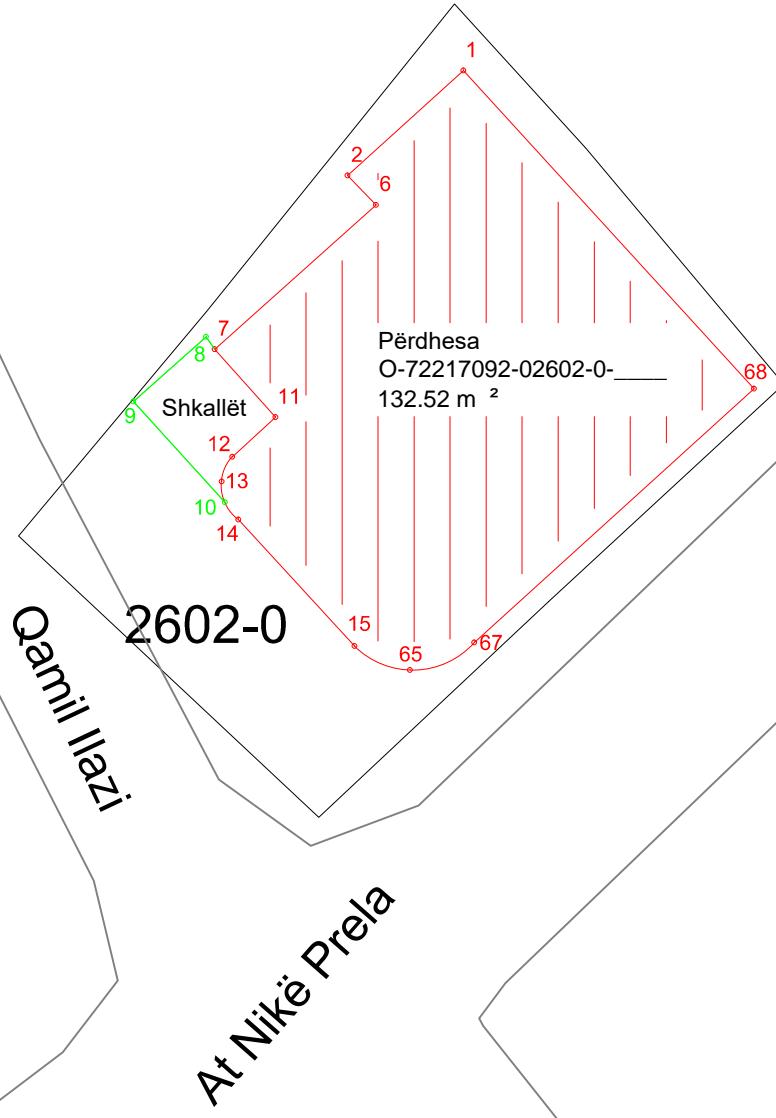

| Nr. | Y | X | H | D | Etazhi | Sqarim | Sipërfaqja (m ²) |
|------------------|------------|------------|--------|----------|----------|----------|------------------------------|
| 1 | 7513135.57 | 4691722.87 | 620.11 | PERDHESA | Përdhesa | Përdhesa | 125.20 |
| 2 | 7513132.50 | 4691720.10 | 620.11 | PERDHESA | | | |
| 6 | 7513133.26 | 4691719.32 | 620.11 | PERDHESA | | | |
| 7 | 7513128.99 | 4691715.51 | 620.11 | PERDHESA | | | |
| 11 | 7513130.60 | 4691713.71 | 620.11 | PERDHESA | | | |
| 12 | 7513129.45 | 4691712.66 | 620.11 | PERDHESA | | | |
| 13 | 7513129.17 | 4691712.01 | 620.11 | PERDHESA | | | |
| 14 | 7513129.62 | 4691711.00 | 620.11 | PERDHESA | | | |
| 15 | 7513132.69 | 4691707.66 | 620.11 | PERDHESA | | | |
| 65 | 7513134.16 | 4691707.02 | 620.11 | PERDHESA | | | |
| 67 | 7513135.86 | 4691707.75 | 620.11 | PERDHESA | | | |
| 68 | 7513143.25 | 4691714.46 | 620.11 | PERDHESA | | | |
| 8 | 7513128.76 | 4691715.83 | 620.11 | SHKALET | | | |
| 9 | 7513126.84 | 4691714.12 | 620.11 | SHKALET | | | |
| 10 | 7513129.26 | 4691711.46 | 620.11 | SHKALET | | | |
| Gjithsej: | | | | | | | 132.52 |

Rilevoi / Snimio: LIRIDON SEJDIU
(emri dhe mbiemri i gjydetit/kompanisë/ ime i prezime geodeta/ kompanije)Aprovoi / Usvojio: _____
(emri dhe mbiemri i pësonit zyrtar/ ime i prezime sluzbeneg lica)Nr. i licencës / Br. licence: 140

V.V.

Nënshkrimi / Potpis: _____

Nënshkrimi / Potpis: _____

Data e rilevimit / Datum snimanja: 12.04.2021

Data e rilevimit / Datum snimanja: _____

Zyra kadastrale komunale / Opštinska katastarska kancelarija: FerizajNr. i njësisë kadastrale / Br. katastarske jedinice : 2602-0Zona kadastrale / Katastarska zona: Ferizaj

Numri i lëndës / Broj predmeta: _____


Lloji i njësisë kadastrale / Vrsta katastarske jedinice : NdërtesëShkalla e zvoglimit / Razmera plana 1: 200**Republika e Kosovës**

Republika Kosova-Republic of Kosovo

Qeveria -Vlada-Government

Ministria e Mjedisit dhe Planifikimit Hapësinor /Ministarstvo Sredine i Prostornog Planiranja/Ministry of Environment and Spatial Planning

AGJENCIA KADASTRALE E KOSOVËS/KATASTARSKA AGECIJA KOSOVA/KOSOVA CADASTRAL AGENCY

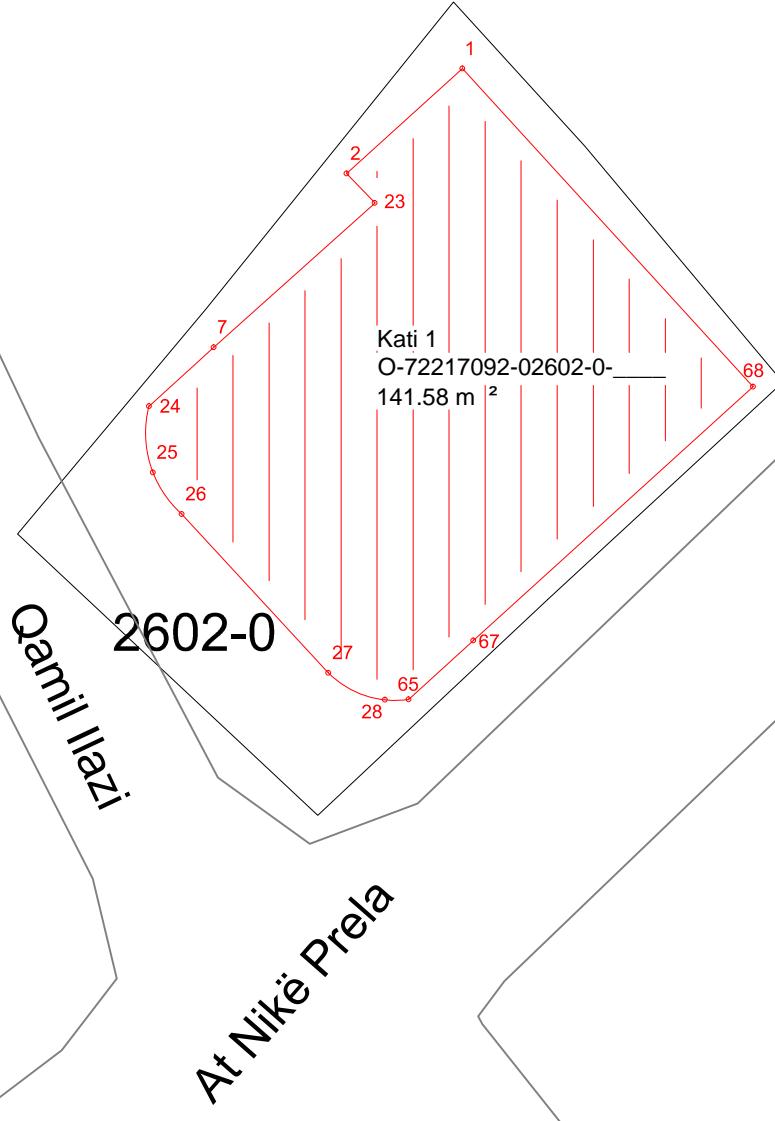

| Nr. | Y | X | H | D | Etazhi | Sqarim | Sipërfaqja (m ²) |
|-----|-------------|-------------|--------|-------|--------|--------|------------------------------|
| 1 | 7513135.568 | 4691722.874 | 623.17 | KATII | | | |
| 2 | 7513132.501 | 4691720.099 | 623.17 | KATII | | | |
| 7 | 7513128.986 | 4691715.505 | 623.17 | KATII | | | |
| 23 | 7513133.25 | 4691719.318 | 623.17 | KATII | | | |
| 24 | 7513127.278 | 4691713.948 | 623.17 | KATII | | | |
| 25 | 7513127.382 | 4691712.191 | 623.17 | KATII | | | |
| 26 | 7513128.142 | 4691711.089 | 623.17 | KATII | | | |
| 27 | 7513132.024 | 4691706.895 | 623.17 | KATII | | | |
| 28 | 7513133.519 | 4691706.18 | 623.17 | KATII | | | |
| 65 | 7513134.144 | 4691706.194 | 623.17 | KATII | | | |
| 67 | 7513135.857 | 4691707.745 | 623.17 | KATII | | | |
| 68 | 7513143.253 | 4691714.464 | 623.17 | KATII | | | |
| | | | | | Katil | Kati 1 | 141.58 |

Rilevoi / Snimio: LIRIDON SEJDIU
(emri dhe mbiemri i gjydetit/kompanisë/ ime i prezime geodeta/ kompanije)Aprovoi / Usvojio: _____
(emri dhe mbiemri i pësonit zyrtar/ ime i prezime sluzbeneg lica)Nr. i licencës / Br. licence: 140

V.V.

Nënshkrimi / Potpis: _____

Nënshkrimi / Potpis: _____

Data e rilevimit / Datum snimanja: 12.04.2021

Data e rilevimit / Datum snimanja: _____


Zyra kadastrale komunale / Opštinska katastarska kancelarija: FerizajNr. i njësisë kadastrale / Br. katastarske jedinice : 2602-0Zona kadastrale / Katastarska zona: Ferizaj

Numri i lëndës / Broj predmeta: _____

Lloji i njësisë kadastrale / Vrsta katastarske jedinice : Ndërtesë

Republika e Kosovës
Republika Kosova-Republic of Kosovo
Qeveria -Vlada-Government

Ministria e Mjedisit dhe Planifikimit Hapësinor /Ministarstvo Sredine i Prostornog Planiranja/Ministry of Environment and Spatial Planning
 AGJENCIA KADASTRALE E KOSOVËS/KATASTARSKA AGENCIJA KOSOVA/KOSOVA CADASTRAL AGENCY

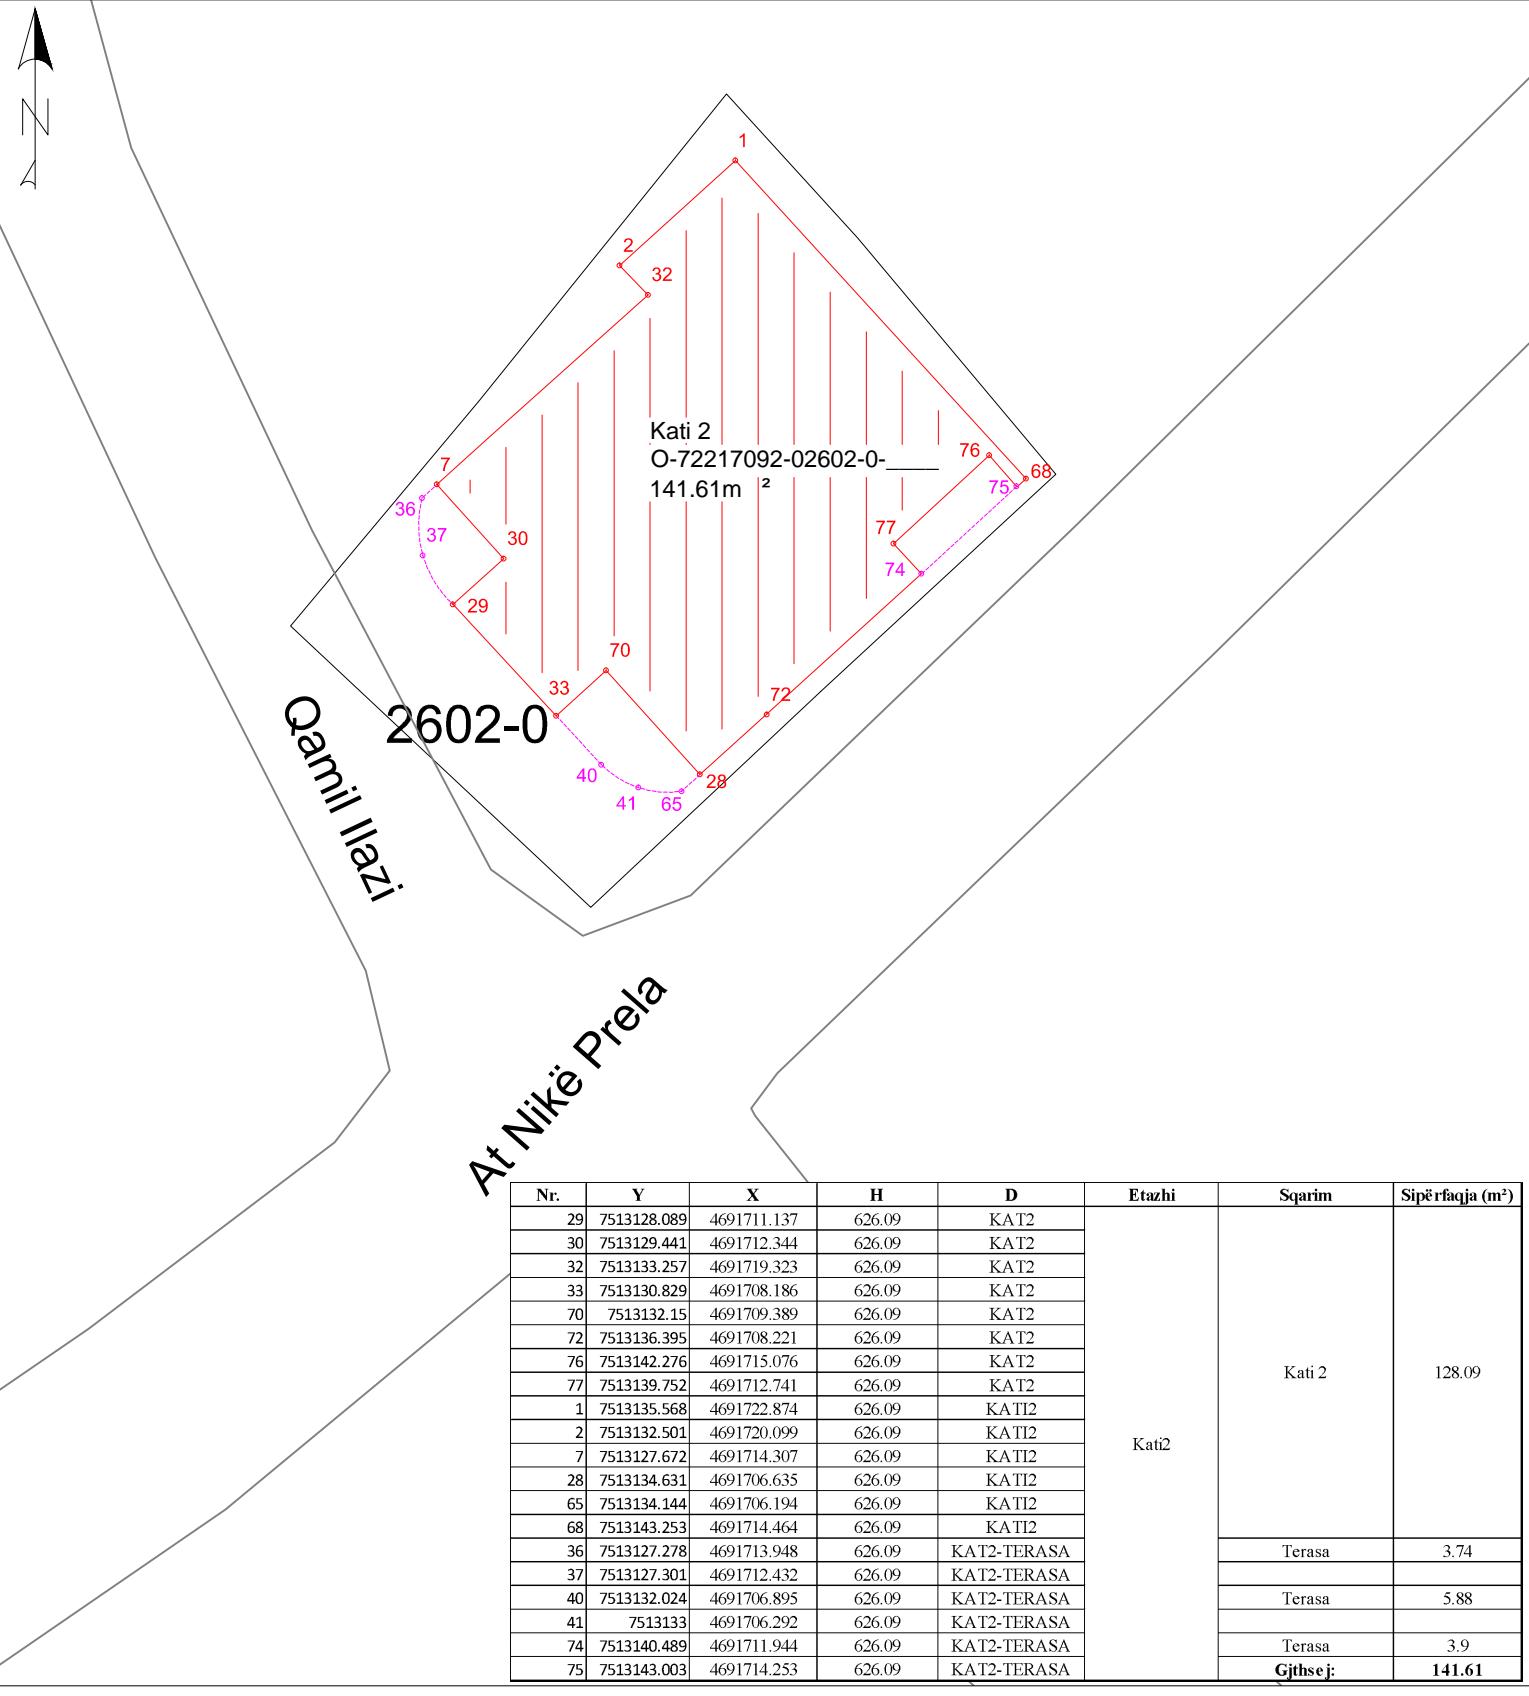Rilevoi / Snimio: LIRIDON SEJDIU
 (emri dhe mbiemri i gjyqetarit/kompanisë/ ime i prezime geodeta/ kompanije)Aprovoi / Usvojio: _____
 (emri dhe mbiemri i pësonit zyrtar/ ime i prezime sluzbeneg lica)Nr. i licencës / Br. licence: 140

V.V.

Nënshkrimi / Potpis: _____

Nënshkrimi / Potpis: _____

Data e rilevimit / Datum snimanja: 12.04.2021

Data e rilevimit / Datum snimanja: _____

Zyra kadastrale komunale / Opštinska katastarska kancelarija: FerizajNr. i njësisë kadastrale / Br. katastarske jedinice : 2602-0Zona kadastrale / Katastarska zona: Ferizaj

Numri i lëndës / Broj predmeta: _____


Lloji i njësisë kadastrale / Vrsta katastarske jedinice : NdërtesëShkalla e zvoglimit / Razmera plana 1: 200**Republika e Kosovës**

Republika Kosova-Republic of Kosovo

Qeveria -Vlada-Government

Ministria e Mjedisit dhe Planifikimit Hapësinor /Ministarstvo Sredine i Prostornog Planiranja/Ministry of Environment and Spatial Planning

AGJENCIA KADASTRALE E KOSOVËS/KATASTARSKA AGECIJA KOSOVA/KOSOVA CADASTRAL AGENCY

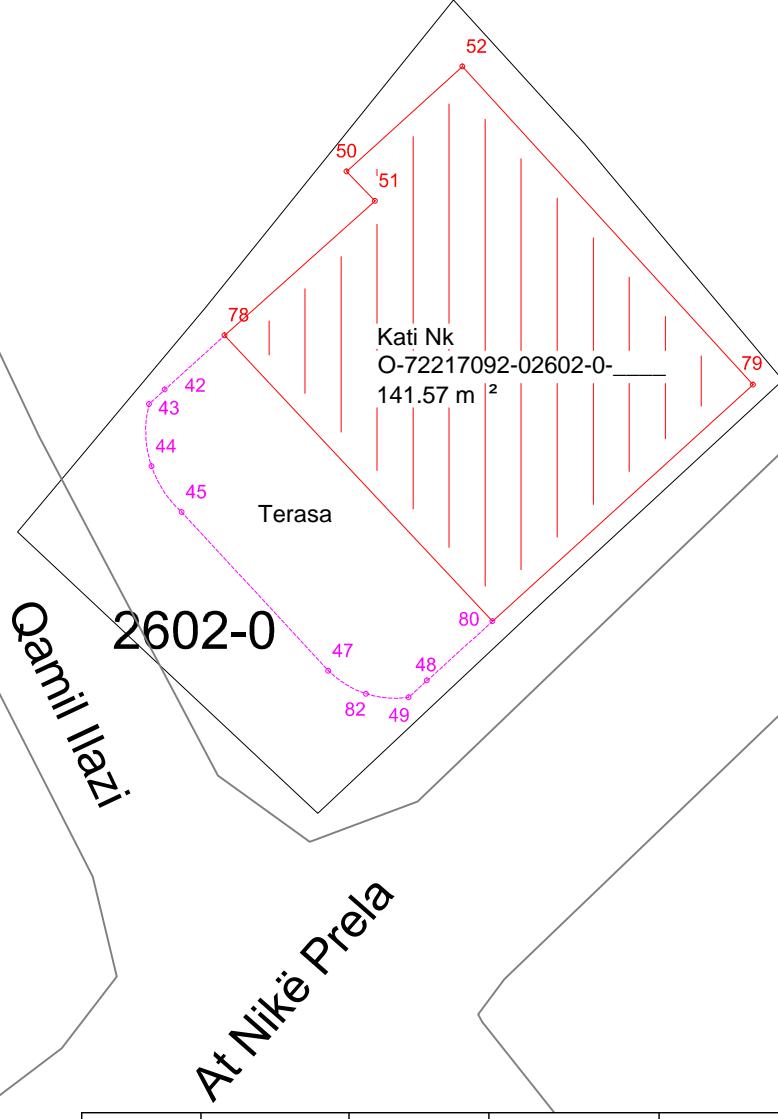

| Nr. | Y | X | H | D | Etazhi | Sqarim | Sipërfaqja (m ²) |
|-----|-------------|-------------|--------|-------------|----------|----------|------------------------------|
| 50 | 7513132.501 | 4691720.099 | 629.30 | KAT3 | Nënku lm | 101.28 | |
| 51 | 7513133.257 | 4691719.323 | 629.30 | KAT3 | | | |
| 52 | 7513135.568 | 4691722.874 | 629.30 | KAT3 | | | |
| 78 | 7513129.28 | 4691715.768 | 629.30 | KAT3 | | | |
| 79 | 7513143.253 | 4691714.464 | 629.30 | KAT3 | | | |
| 80 | 7513136.36 | 4691708.202 | 629.30 | KAT3-TERAS | Nënku lm | 40.29 | |
| 82 | 7513133.018 | 4691706.286 | 629.30 | KAT3-TERAS | | | |
| 42 | 7513127.698 | 4691714.331 | 629.30 | KAT3-TERASA | | | |
| 43 | 7513127.278 | 4691713.948 | 629.30 | KAT3-TERASA | | | |
| 44 | 7513127.344 | 4691712.304 | 629.30 | KAT3-TERASA | | | |
| 45 | 7513128.142 | 4691711.089 | 629.30 | KAT3-TERASA | | | |
| 47 | 7513132.024 | 4691706.895 | 629.30 | KAT3-TERASA | | | |
| 48 | 7513134.631 | 4691706.635 | 629.30 | KAT3-TERASA | | | |
| 49 | 7513134.144 | 4691706.194 | 629.30 | KAT3-TERASA | | | |
| | | | | | | Gjithsej | 141.57 |

Rilevoi / Snimio: LIRIDON SEJDIU
(emri dhe mbiemri i gjydetit/kompanisë/ ime i prezime geodeta/ kompanije)Aprovoi / Usvojio: _____
(emri dhe mbiemri i pësonit zyrtar/ ime i prezime sluzbeneg lica)Nr. i licencës / Br. licence: 140

V.V.

Nënshtkrimi / Potpis: _____

Nënshtkrimi / Potpis: _____

Data e rilevimit / Datum snimanja: 12.04.2021

Data e rilevimit / Datum snimanja: _____



Republika e Kosovës

Republika Kosova-Republic of Kosovo

Qeveria e Kosovës- Vlada Kosova- Government of Kosovo

Ministria e Infrastrukturës dhe Ambientit/ Ministrastvo Infrastrukture i Sredine/ Ministry of Infrastructure and Environment
AGJENCIA KADASTRALE E KOSOVËS/KOSOVSKA KATASTARSKA AGENCIA/ KOSOVO CADASTRAL AGENCY

Komuna: Ferizaj
Numri i njësis kadastrale: 02606-0

Zona Kadastrale: Ferizaj
Sistemi koordinat: KosovaRef01

| Nr. | Y | X | H | D | Etazhi | Sqarim | Sipërfaqja (m ²) |
|-----|------------|------------|--------|----------|-----------|--------|------------------------------|
| 1 | 7513135.57 | 4691722.87 | 620.11 | PERDHESA | | | |
| 2 | 7513132.50 | 4691720.10 | 620.11 | PERDHESA | | | |
| 6 | 7513133.26 | 4691719.32 | 620.11 | PERDHESA | | | |
| 7 | 7513128.99 | 4691715.51 | 620.11 | PERDHESA | | | |
| 11 | 7513130.60 | 4691713.71 | 620.11 | PERDHESA | | | |
| 12 | 7513129.45 | 4691712.66 | 620.11 | PERDHESA | | | |
| 13 | 7513129.17 | 4691712.01 | 620.11 | PERDHESA | | | |
| 14 | 7513129.62 | 4691711.00 | 620.11 | PERDHESA | | | |
| 15 | 7513132.69 | 4691707.66 | 620.11 | PERDHESA | | | |
| 65 | 7513134.16 | 4691707.02 | 620.11 | PERDHESA | | | |
| 67 | 7513135.86 | 4691707.75 | 620.11 | PERDHESA | | | |
| 68 | 7513143.25 | 4691714.46 | 620.11 | PERDHESA | | | |
| 8 | 7513128.76 | 4691715.83 | 620.11 | SHKALET | | | |
| 9 | 7513126.84 | 4691714.12 | 620.11 | SHKALET | | | |
| 10 | 7513129.26 | 4691711.46 | 620.11 | SHKALET | | | |
| | | | | | Gjithsej: | | 132.52 |

| Nr. | Y | X | H | D | Etazhi | Sqarim | Sipërfaqja (m ²) |
|-----|-------------|-------------|--------|-------|--------|--------|------------------------------|
| 1 | 7513135.568 | 4691722.874 | 623.17 | KATI1 | | | |
| 2 | 7513132.501 | 4691720.099 | 623.17 | KATI1 | | | |
| 7 | 7513128.986 | 4691715.505 | 623.17 | KATI1 | | | |
| 23 | 7513133.25 | 4691719.318 | 623.17 | KATI1 | | | |
| 24 | 7513127.278 | 4691713.948 | 623.17 | KATI1 | | | |
| 25 | 7513127.382 | 4691712.191 | 623.17 | KATI1 | | | |
| 26 | 7513128.142 | 4691711.089 | 623.17 | KATI1 | | | |
| 27 | 7513132.024 | 4691706.895 | 623.17 | KATI1 | | | |
| 28 | 7513133.519 | 4691706.18 | 623.17 | KATI1 | | | |
| 65 | 7513134.144 | 4691706.194 | 623.17 | KATI1 | | | |
| 67 | 7513135.857 | 4691707.745 | 623.17 | KATI1 | | | |
| 68 | 7513143.253 | 4691714.464 | 623.17 | KATI1 | | | |
| | | | | | Kati 1 | | 141.58 |

| Nr. | Y | X | H | D | Etazhi | Sqarim | Sipërfaqja (m ²) |
|-----|-------------|-------------|--------|-------------|-----------|--------|------------------------------|
| 29 | 7513128.089 | 4691711.137 | 626.09 | KAT2 | | | |
| 30 | 7513129.441 | 4691712.344 | 626.09 | KAT2 | | | |
| 32 | 7513133.257 | 4691719.323 | 626.09 | KAT2 | | | |
| 33 | 7513130.829 | 4691708.186 | 626.09 | KAT2 | | | |
| 70 | 7513132.15 | 4691709.389 | 626.09 | KAT2 | | | |
| 72 | 7513136.395 | 4691708.221 | 626.09 | KAT2 | | | |
| 76 | 7513142.276 | 4691715.076 | 626.09 | KAT2 | | | |
| 77 | 7513139.752 | 4691712.741 | 626.09 | KAT2 | | | |
| 1 | 7513135.568 | 4691722.874 | 626.09 | KATI2 | | | |
| 2 | 7513132.501 | 4691720.099 | 626.09 | KATI2 | | | |
| 7 | 7513127.672 | 4691714.307 | 626.09 | KATI2 | | | |
| 28 | 7513134.631 | 4691706.635 | 626.09 | KATI2 | | | |
| 65 | 7513134.144 | 4691706.194 | 626.09 | KATI2 | | | |
| 68 | 7513143.253 | 4691714.464 | 626.09 | KATI2 | | | |
| 36 | 7513127.278 | 4691713.948 | 626.09 | KAT2-TERASA | | | |
| 37 | 7513127.301 | 4691712.432 | 626.09 | KAT2-TERASA | | | |
| 40 | 7513132.024 | 4691706.895 | 626.09 | KAT2-TERASA | | | |
| 41 | 7513133 | 4691706.292 | 626.09 | KAT2-TERASA | | | |
| 74 | 7513140.489 | 4691711.944 | 626.09 | KAT2-TERASA | | | |
| 75 | 7513143.003 | 4691714.253 | 626.09 | KAT2-TERASA | | | |
| | | | | | Terasa | | 3.74 |
| | | | | | | | |
| | | | | | Terasa | | 5.88 |
| | | | | | | | |
| | | | | | Terasa | | 3.9 |
| | | | | | | | |
| | | | | | Gjithsej: | | 141.61 |

| | | | |
|---|----------------|----------------------|--|
| Gjeodeti / Kompania gjeodete e licencuar: | Liridon Sejdiu | Nënshkrimi dhe vula: | |
| Numri i licencës | 140 | | |



Republika e Kosovës
Republika Kosova-Republic of Kosovo
Qeveria e Kosovës- Vlada Kosova- Government of Kosovo
Ministria e Infrastrukturës dhe Ambientit/ Ministrastvo Infrastrukture i Sredine/ Ministry of Infrastructure and Environment

| | |
|---|---------------------------------------|
| Komuna: Ferizaj | Zona Kadastrale: Ferizaj |
| Numri i njësis kadastrale: 02606-0 | Sistemi koordinat: KosovaRef01 |

| Nr. | Y | X | H | D | Etazhi | Sqarim | Sipërfa qja (m ²) |
|-----|-------------|-------------|--------|-------------|---------|----------|-------------------------------|
| 50 | 7513132.501 | 4691720.099 | 629.30 | KAT3 | Nënkulm | Nënkulm | 101.28 |
| 51 | 7513133.257 | 4691719.323 | 629.30 | KAT3 | | | |
| 52 | 7513135.568 | 4691722.874 | 629.30 | KAT3 | | | |
| 78 | 7513129.28 | 4691715.768 | 629.30 | KAT3 | | | |
| 79 | 7513143.253 | 4691714.464 | 629.30 | KAT3 | | | |
| 80 | 7513136.36 | 4691708.202 | 629.30 | KAT3-TERAS | | | |
| 82 | 7513133.018 | 4691706.286 | 629.30 | KAT3-TERAS | | | |
| 42 | 7513127.698 | 4691714.331 | 629.30 | KAT3-TERASA | | | |
| 43 | 7513127.278 | 4691713.948 | 629.30 | KAT3-TERASA | | | |
| 44 | 7513127.344 | 4691712.304 | 629.30 | KAT3-TERASA | | | |
| 45 | 7513128.142 | 4691711.089 | 629.30 | KAT3-TERASA | | | |
| 47 | 7513132.024 | 4691706.895 | 629.30 | KAT3-TERASA | | | |
| 48 | 7513134.631 | 4691706.635 | 629.30 | KAT3-TERASA | | | |
| 49 | 7513134.144 | 4691706.194 | 629.30 | KAT3-TERASA | | Gjithsej | 141.57 |


| | | | |
|---|----------------|----------------------|--|
| Gjeodeti / Kompania gjeodete e licencuar: | Liridon Sejdiu | Nënshkrimi dhe vula: | |
| Numri i licencës | 140 | | |

Zyra kadastrale komunale / Opštinska katastarska kancelarija: FerizajNr. i njësisë kadastrale / Br. katastarske jedinice : 2602-Zona kadastrale / Katastarska zona: Ferizaj

Numri i lëndës / Broj predmeta: _____

Lloji i njësisë kadastrale / Vrsta katastarske jedinice : Ndërtesë**Republika e Kosovës****Republika Kosova-Republic of Kosovo****Qeveria -Vlada-Government****Ministria e Mjedisit dhe Planifikimit Hapësinor /Ministarstvo Sredine i Prostornog Planiranja/Ministry of Environment and Spatial Planning**

AGJENCIA KADASTRALE E KOSOVËS/KATASTARSKA AGECIJA KOSOVA/KOSOVA CADASTRAL AGENCY

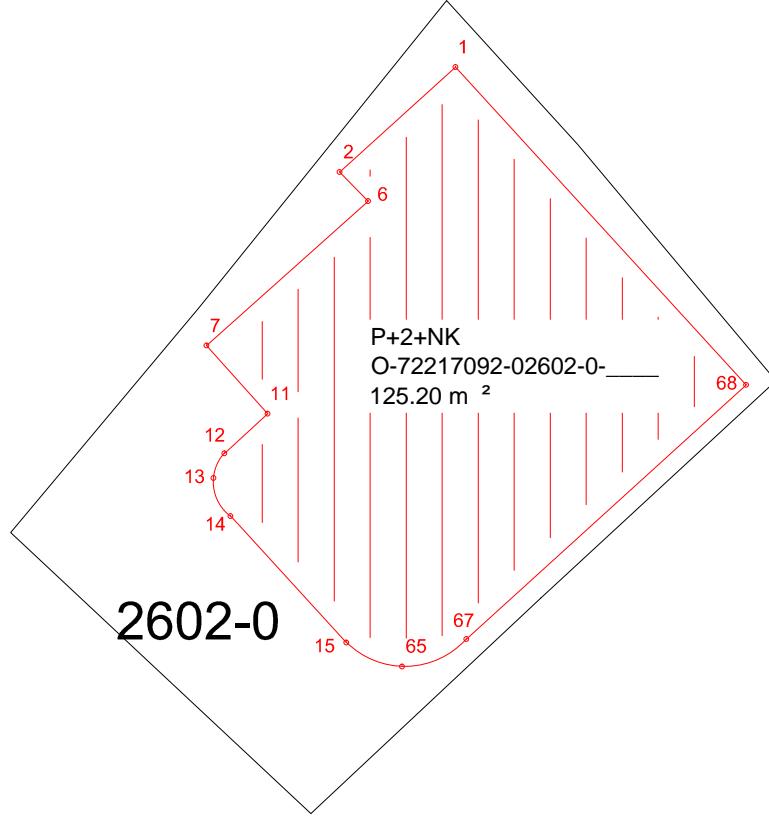

| Nr | Y | X | H | Kodi | Përvitimi | Burimi |
|----|-------------|-------------|---------|------|-----------------|--------|
| 1 | 7513135.568 | 4691722.874 | 620.112 | 40 | Shtëpi-Ndërtesë | PM |
| 2 | 7513132.501 | 4691720.099 | 620.112 | 40 | Shtëpi-Ndërtesë | PM |
| 6 | 7513133.257 | 4691719.323 | 620.112 | 40 | Shtëpi-Ndërtesë | PM |
| 7 | 7513128.986 | 4691715.505 | 620.112 | 40 | Shtëpi-Ndërtesë | PM |
| 11 | 7513130.596 | 4691713.706 | 620.112 | 40 | Shtëpi-Ndërtesë | PM |
| 12 | 7513129.454 | 4691712.656 | 620.112 | 40 | Shtëpi-Ndërtesë | PM |
| 13 | 7513129.172 | 4691712.005 | 620.112 | 40 | Shtëpi-Ndërtesë | PM |
| 14 | 7513129.620 | 4691710.995 | 620.112 | 40 | Shtëpi-Ndërtesë | PM |
| 15 | 7513132.685 | 4691707.655 | 620.112 | 40 | Shtëpi-Ndërtesë | PM |
| 65 | 7513134.155 | 4691707.022 | 620.112 | 40 | Shtëpi-Ndërtesë | PM |
| 67 | 7513135.857 | 4691707.745 | 620.112 | 40 | Shtëpi-Ndërtesë | PM |
| 68 | 7513143.253 | 4691714.464 | 620.112 | 40 | Shtëpi-Ndërtesë | PM |

Rilevoi / Snimio: LIRIDON SEJDIU
(emri dhe mbiemri i gjyqetarit/kompanisë/ ime i prezime geodeta/ kompanije)

Aprovoi / Usvojo: _____

(emri dhe mbiemri i pësonit zyrtar/ ime i prezime sluzbeneg lica)

Nr. i licencës / Br. licence: 140

V.V.

Nënshkrimi / Potpis: _____

Nënshkrimi / Potpis: _____

Data e rilevimit / Datum snimanja: 12.04.2021

Data e rilevimit / Datum snimanja: _____



Republika e Kosovës

Republika Kosova - Republic of Kosovo

Qeveria e Kosovës - Vlada Kosova - Government of Kosovo

Ministria e Infrastrukturës dhe Ambientit/ Ministrastvo Infrastrukture i Sredine/ Ministry of Infrastructure and Environment
AGJENCIA KADASTRALE E KOSOVËS/ KOSOVSKA KATASTARSKA AGENCIJA/ KOSOVA CADASTRAL AGENCY

| R E G J I S T R I M I I NDERTESËS / SHTËPISË | | | | | | | | | | | | | |
|--|---------|-----------------|----------------------------|------------|--|--|---|---------------------------|-----------------|----------------------|--|-----------------|----------------|
| Nr | Komuna | Zona Kadastrale | Numri i ndërtesës (njësia) | Etazhiteti | Katet | Sipërfaqja e kateve [m ²] | Sipërfaqja e bazamentit [m ²] | Adresa e Njësisë | Vendi i quajtur | Shfrytëzimi i aktual | Pronari / Shfrytëzuesi Emri (Emri i prindit) Mbiemri | Numri përsoneal | Pjesa e Pronës |
| 1 | Ferizaj | Ferizaj | O-72217092-02602-0-____- | P+2+NK | Përdhesa Kati 1 Kati 2 Nërkulm Gjithsej: | 132.52 141.58 141.61 141.57 557.28 | 125.2 | Rr. " AT NIKPRELAJ" nr 47 | AT NIKPRELAJ | Afarizëm/Banim | Albnor (Gazemend) Shehu | 1233339128 | 1/1 |

Gjeodeti/kompania e licencuar: LIRIDON SEJDIU

Nr i licencës: 140

Nënshkrimi dhe vula:

Zyra kadastrale komunale / Opštinska katastarska kancelarija: Ferizaj



Nr. i njësisë kadastrale / Br. katastarske jedinice : 2602-0

Zona kadastrale / Katastarska zona: Ferizaj

Numri i lëndës / Broj predmeta: _____

Lloji i njësisë kadastrale / Vrsta katastarske jedinice : Ndërtesë

Shkalla e zvoglimit / Razmera plana 1: 200


Republika e Kosovës

Republika Kosova-Republic of Kosovo

Qeveria -Vlada-Government

Ministria e Mjedisit dhe Planifikimit Hapësinor /Ministarstvo Sredine i Prostornog Planiranja/Ministry of Environment and Spatial Planning

AGJENCIA KADASTRALE E KOSOVËS/KATASTARSKA AGECIJA KOSOVA/KOSOVA CADASTRAL AGENCY

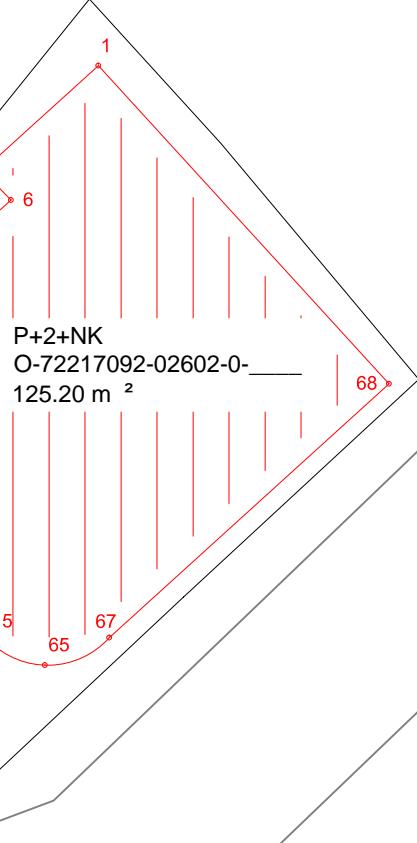

| Nr | Y | X | H | Kodi | Përkrimi | Burimi |
|----|-------------|-------------|---------|------|-----------------|--------|
| 1 | 7513135.568 | 4691722.874 | 620.112 | 40 | Shtëpi-Ndërtesë | PM |
| 2 | 7513132.501 | 4691720.099 | 620.112 | 40 | Shtëpi-Ndërtesë | PM |
| 6 | 7513133.257 | 4691719.323 | 620.112 | 40 | Shtëpi-Ndërtesë | PM |
| 7 | 7513128.986 | 4691715.505 | 620.112 | 40 | Shtëpi-Ndërtesë | PM |
| 11 | 7513130.596 | 4691713.706 | 620.112 | 40 | Shtëpi-Ndërtesë | PM |
| 12 | 7513129.454 | 4691712.656 | 620.112 | 40 | Shtëpi-Ndërtesë | PM |
| 13 | 7513129.172 | 4691712.005 | 620.112 | 40 | Shtëpi-Ndërtesë | PM |
| 14 | 7513129.620 | 4691710.995 | 620.112 | 40 | Shtëpi-Ndërtesë | PM |
| 15 | 7513132.685 | 4691707.655 | 620.112 | 40 | Shtëpi-Ndërtesë | PM |
| 65 | 7513134.155 | 4691707.022 | 620.112 | 40 | Shtëpi-Ndërtesë | PM |
| 67 | 7513135.857 | 4691707.745 | 620.112 | 40 | Shtëpi-Ndërtesë | PM |
| 68 | 7513143.253 | 4691714.464 | 620.112 | 40 | Shtëpi-Ndërtesë | PM |
| 8 | 7513128.764 | 4691715.831 | 620.112 | 40 | Shtëpi-Ndërtesë | PM |
| 9 | 7513126.840 | 4691714.119 | 620.112 | 40 | Shtëpi-Ndërtesë | PM |
| 10 | 7513129.257 | 4691711.459 | 620.112 | 40 | Shtëpi-Ndërtesë | PM |
| 98 | 7513129.791 | 4691714.606 | 620.112 | 40 | Shtëpi-Ndërtesë | PM |
| 98 | 7513129.791 | 4691714.606 | 620.112 | - | Hyrje | PM |

Rilevoi / Snimio: LIRIDON SEJDIU
(emri dhe mbiemri i gjyqetarit/kompanisë/ ime i prezime geodeta/ kompanije)

Aprovoi / Usvojio: _____
(emri dhe mbiemri i pësonit zyrtar/ ime i prezime sluzbenog lica)

Nr. i licencës / Br. licence: 140

V.V.

Nënshkrimi / Potpis: _____

Nënshkrimi / Potpis: _____

Data e rilevimit / Datum snimanja: 12.04.2021

Data e rilevimit / Datum snimanja: _____

Zyra kadastrale komunale / Opštinska katastarska kancelarija: FerizajNr. i njësisë kadastrale / Br. katastarske jedinice : 2602-0Zona kadastrale / Katastarska zona: Ferizaj

Numri i lëndës / Broj predmeta: _____


Lloji i njësisë kadastrale / Vrsta katastarske jedinice : Pjesë e ndërtesës**Republika e Kosovës**

Republika Kosova-Republic of Kosovo

Qeveria -Vlada-Government

Ministria e Mjedisit dhe Planifikimit Hapësinor /Ministarstvo Sredine i Prostornog Planiranja/Ministry of Environment and Spatial Planning

AGJENCIA KADASTRALE E KOSOVËS/KATASTARSKA AGECIJA KOSOVA/KOSOVA CADASTRAL AGENCY

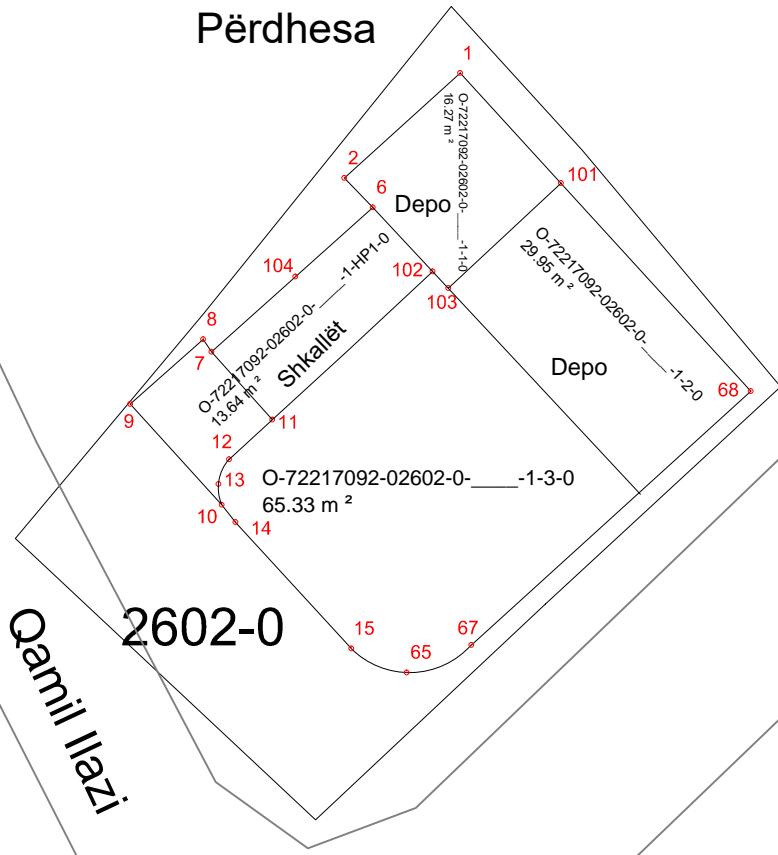Përdhesa**At Nikë Prela****Qamil Ilazi**

| Nr | Y | X | h | Etazhi | Përshkrimi |
|---------|------------|------------|---|----------|-------------------|
| 1 | 7513135.57 | 4691722.87 | | | Pjesë e ndërteses |
| 2 | 7513132.50 | 4691720.10 | | | Pjesë e ndërteses |
| 6 | 7513133.26 | 4691719.32 | | | Pjesë e ndërteses |
| 7 | 7513128.99 | 4691715.51 | | | Pjesë e ndërteses |
| 11 | 7513130.60 | 4691713.71 | | | Pjesë e ndërteses |
| 12 | 7513129.45 | 4691712.66 | | | Pjesë e ndërteses |
| 13 | 7513129.17 | 4691712.01 | | | Pjesë e ndërteses |
| 14 | 7513129.62 | 4691711.00 | | | Pjesë e ndërteses |
| 15 | 7513132.69 | 4691707.66 | | | Pjesë e ndërteses |
| 65 | 7513134.16 | 4691707.02 | | | Pjesë e ndërteses |
| 67 | 7513135.86 | 4691707.75 | | | Pjesë e ndërteses |
| 68 | 7513143.25 | 4691714.46 | | | Pjesë e ndërteses |
| 101 | 7513138.23 | 4691719.96 | | | Pjesë e ndërteses |
| 102 | 7513134.83 | 4691717.63 | | | Pjesë e ndërteses |
| 103 | 7513135.25 | 4691717.19 | | | Pjesë e ndërteses |
| 104 | 7513131.21 | 4691717.49 | | | Pjesë e ndërteses |
| 8 | 7513128.76 | 4691715.83 | | | Pjesë e ndërteses |
| 9 | 7513126.84 | 4691714.12 | | | Pjesë e ndërteses |
| 10 | 7513129.26 | 4691711.46 | | | Pjesë e ndërteses |
| 620.112 | | | | Përdhesa | |

Rilevoi / Snimio: LIRIDON SEJDIU
(emri dhe mbiemri i gjyqetarit/kompanisë/ ime i prezime geodeta/ kompanije)Aprovoi / Usvojio: _____
(emri dhe mbiemri i pësonit zyrtar/ ime i prezime sluzbenog lica)Nr. i licencës / Br. licence: 140


V.V.

Nënshkrimi / Potpis: _____

Nënshkrimi / Potpis: _____

Data e rilevimit / Datum snimanja: 12.04.2021

Data e rilevimit / Datum snimanja: _____

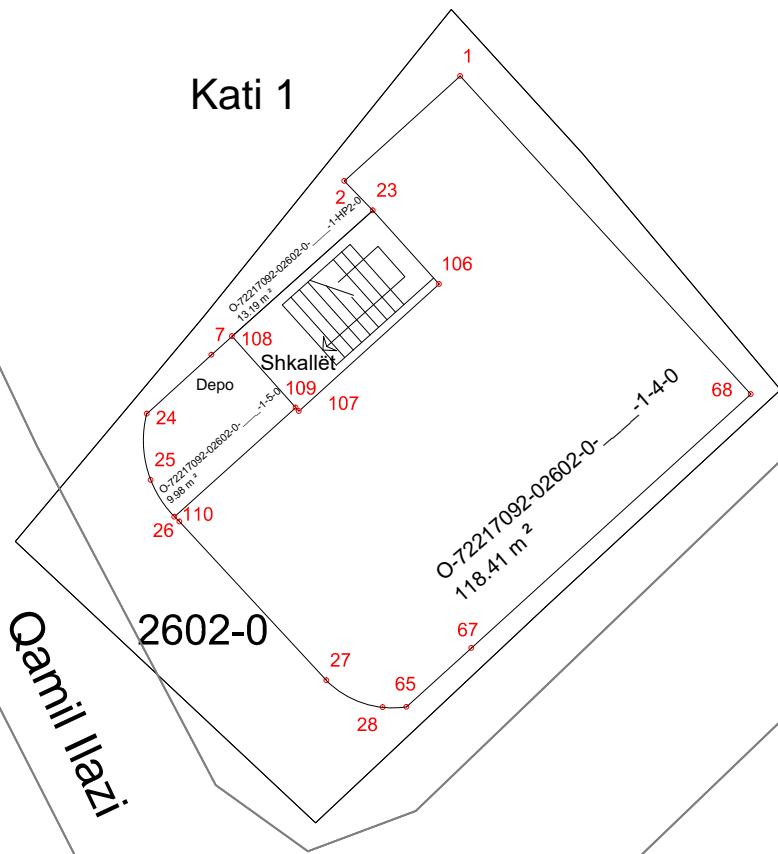**Kati 1****Qamil Ilazi****At Nikë Prela**

| Nr | Y | X | h | Etazhi | Përshkrimi |
|---------|------------|------------|---|--------|-------------------|
| 1 | 7513135.57 | 4691722.87 | | | Pjesë e ndërteses |
| 2 | 7513132.50 | 4691720.10 | | | Pjesë e ndërteses |
| 7 | 7513128.99 | 4691715.51 | | | Pjesë e ndërteses |
| 23 | 7513133.25 | 4691719.32 | | | Pjesë e ndërteses |
| 24 | 7513127.28 | 4691713.95 | | | Pjesë e ndërteses |
| 25 | 7513127.38 | 4691712.19 | | | Pjesë e ndërteses |
| 26 | 7513128.14 | 4691711.09 | | | Pjesë e ndërteses |
| 27 | 7513132.02 | 4691706.90 | | | Pjesë e ndërteses |
| 28 | 7513133.52 | 4691706.18 | | | Pjesë e ndërteses |
| 65 | 7513134.14 | 4691706.19 | | | Pjesë e ndërteses |
| 67 | 7513135.86 | 4691707.75 | | | Pjesë e ndërteses |
| 68 | 7513143.25 | 4691714.46 | | | Pjesë e ndërteses |
| 106 | 7513135.00 | 4691717.37 | | | Pjesë e ndërteses |
| 107 | 7513131.30 | 4691714.01 | | | Pjesë e ndërteses |
| 108 | 7513129.53 | 4691715.99 | | | Pjesë e ndërteses |
| 109 | 7513131.21 | 4691714.11 | | | Pjesë e ndërteses |
| 110 | 7513128.01 | 4691711.22 | | | Pjesë e ndërteses |
| 623.174 | | | | | KAT1 |

Rilevoi / Snimio: LIRIDON SEJDIU
(emri dhe mbiemri i gjyqetarit/kompanisë/ ime i prezime geodeta/ kompanije)Aprovoi / Usvojio: _____
(emri dhe mbiemri i pësonit zyrtar/ ime i prezime sluzbenog lica)Nr. i licencës / Br. licence: 140

V.V.

Nënshkrimi / Potpis: _____

Nënshkrimi / Potpis: _____

Data e rilevimit / Datum snimanja: 12.04.2021

Data e rilevimit / Datum snimanja: _____

Zyra kadastrale komunale / Opštinska katastarska kancelarija: Ferizaj



Nr. i njësisë kadastrale / Br. katastarske jedinice : 2602-0

Zona kadastrale / Katastarska zona: Ferizaj

Numri i lëndës / Broj predmeta: _____

Lloji i njësisë kadastrale / Vrsta katastarske jedinice : Pjesë e ndërtesës

Shkalla e zvoglimit / Razmera plana 1: 200

Republika e Kosovës

Republika Kosova-Republic of Kosovo

Qeveria -Vlada-Government

Ministria e Mjedisit dhe Planifikimit Hapësinor /Ministarstvo Sredine i Prostornog Planiranja/Ministry of Environment and Spatial Planning

AGJENCIA KADASTRALE E KOSOVËS/KATASTARSKA AGECIJA KOSOVA/KOSOVA CADASTRAL AGENCY

Kati 2

Qamil Ilazi

At Nikë Prela

2602-0

O-72217092-02602-0-____-1-6-0
118.41 m²

O-72217092-02602-0-____-1-PH3-0
13.19 m²

7 108
Depo
Shkallët
109 107
24
25
26
110
27
65
28
67
106
23
1 2
68

| Nr | Y | X | h | Etazhi | Përshkrimi |
|-----|------------|------------|---|--------|-------------------|
| 1 | 7513135.57 | 4691722.87 | | | Pjesë e ndërteses |
| 2 | 7513132.50 | 4691720.10 | | | Pjesë e ndërteses |
| 7 | 7513128.99 | 4691715.51 | | | Pjesë e ndërteses |
| 23 | 7513133.25 | 4691719.32 | | | Pjesë e ndërteses |
| 24 | 7513127.28 | 4691713.95 | | | Pjesë e ndërteses |
| 25 | 7513127.38 | 4691712.19 | | | Pjesë e ndërteses |
| 26 | 7513128.14 | 4691711.09 | | | Pjesë e ndërteses |
| 27 | 7513132.02 | 4691706.90 | | | Pjesë e ndërteses |
| 28 | 7513133.52 | 4691706.18 | | | Pjesë e ndërteses |
| 65 | 7513134.14 | 4691706.19 | | | Pjesë e ndërteses |
| 67 | 7513135.86 | 4691707.75 | | | Pjesë e ndërteses |
| 68 | 7513143.25 | 4691714.46 | | | Pjesë e ndërteses |
| 106 | 7513135.00 | 4691717.37 | | | Pjesë e ndërteses |
| 107 | 7513131.30 | 4691714.01 | | | Pjesë e ndërteses |
| 108 | 7513129.53 | 4691715.99 | | | Pjesë e ndërteses |
| 109 | 7513131.21 | 4691714.11 | | | Pjesë e ndërteses |
| 110 | 7513128.01 | 4691711.22 | | | Pjesë e ndërteses |

626.094 KATI2

Rilevoi / Snimio: LIRIDON SEJDIU
(emri dhe mbiemri i gjydetit/kompanisë/ ime i prezime geodeta/ kompanije)

Aprovoi / Usvojio: _____
(emri dhe mbiemri i pësonit zyrtar/ ime i prezime sluzbenog lica)

Nr. i licencës / Br. licence: 140

V.V.

Nënshkrimi / Potpis: _____

Nënshkrimi / Potpis: _____

Data e rilevimit / Datum snimanja: 12.04.2021

Data e rilevimit / Datum snimanja: _____

Zyra kadastrale komunale / Opštinska katastarska kancelarija: FerizajNr. i njësisë kadastrale / Br. katastarske jedinice : 2602-0Zona kadastrale / Katastarska zona: Ferizaj

Numri i lëndës / Broj predmeta: _____


Lloji i njësisë kadastrale / Vrsta katastarske jedinice : Pjesë e ndërtesës**Republika e Kosovës**

Republika Kosova-Republic of Kosovo

Qeveria -Vlada-Government

Ministria e Mjedisit dhe Planifikimit Hapësinor /Ministarstvo Sredine i Prostornog Planiranja/Ministry of Environment and Spatial Planning

AGJENCIA KADASTRALE E KOSOVËS/KATASTARSKA AGECIJA KOSOVA/KOSOVA CADASTRAL AGENCY

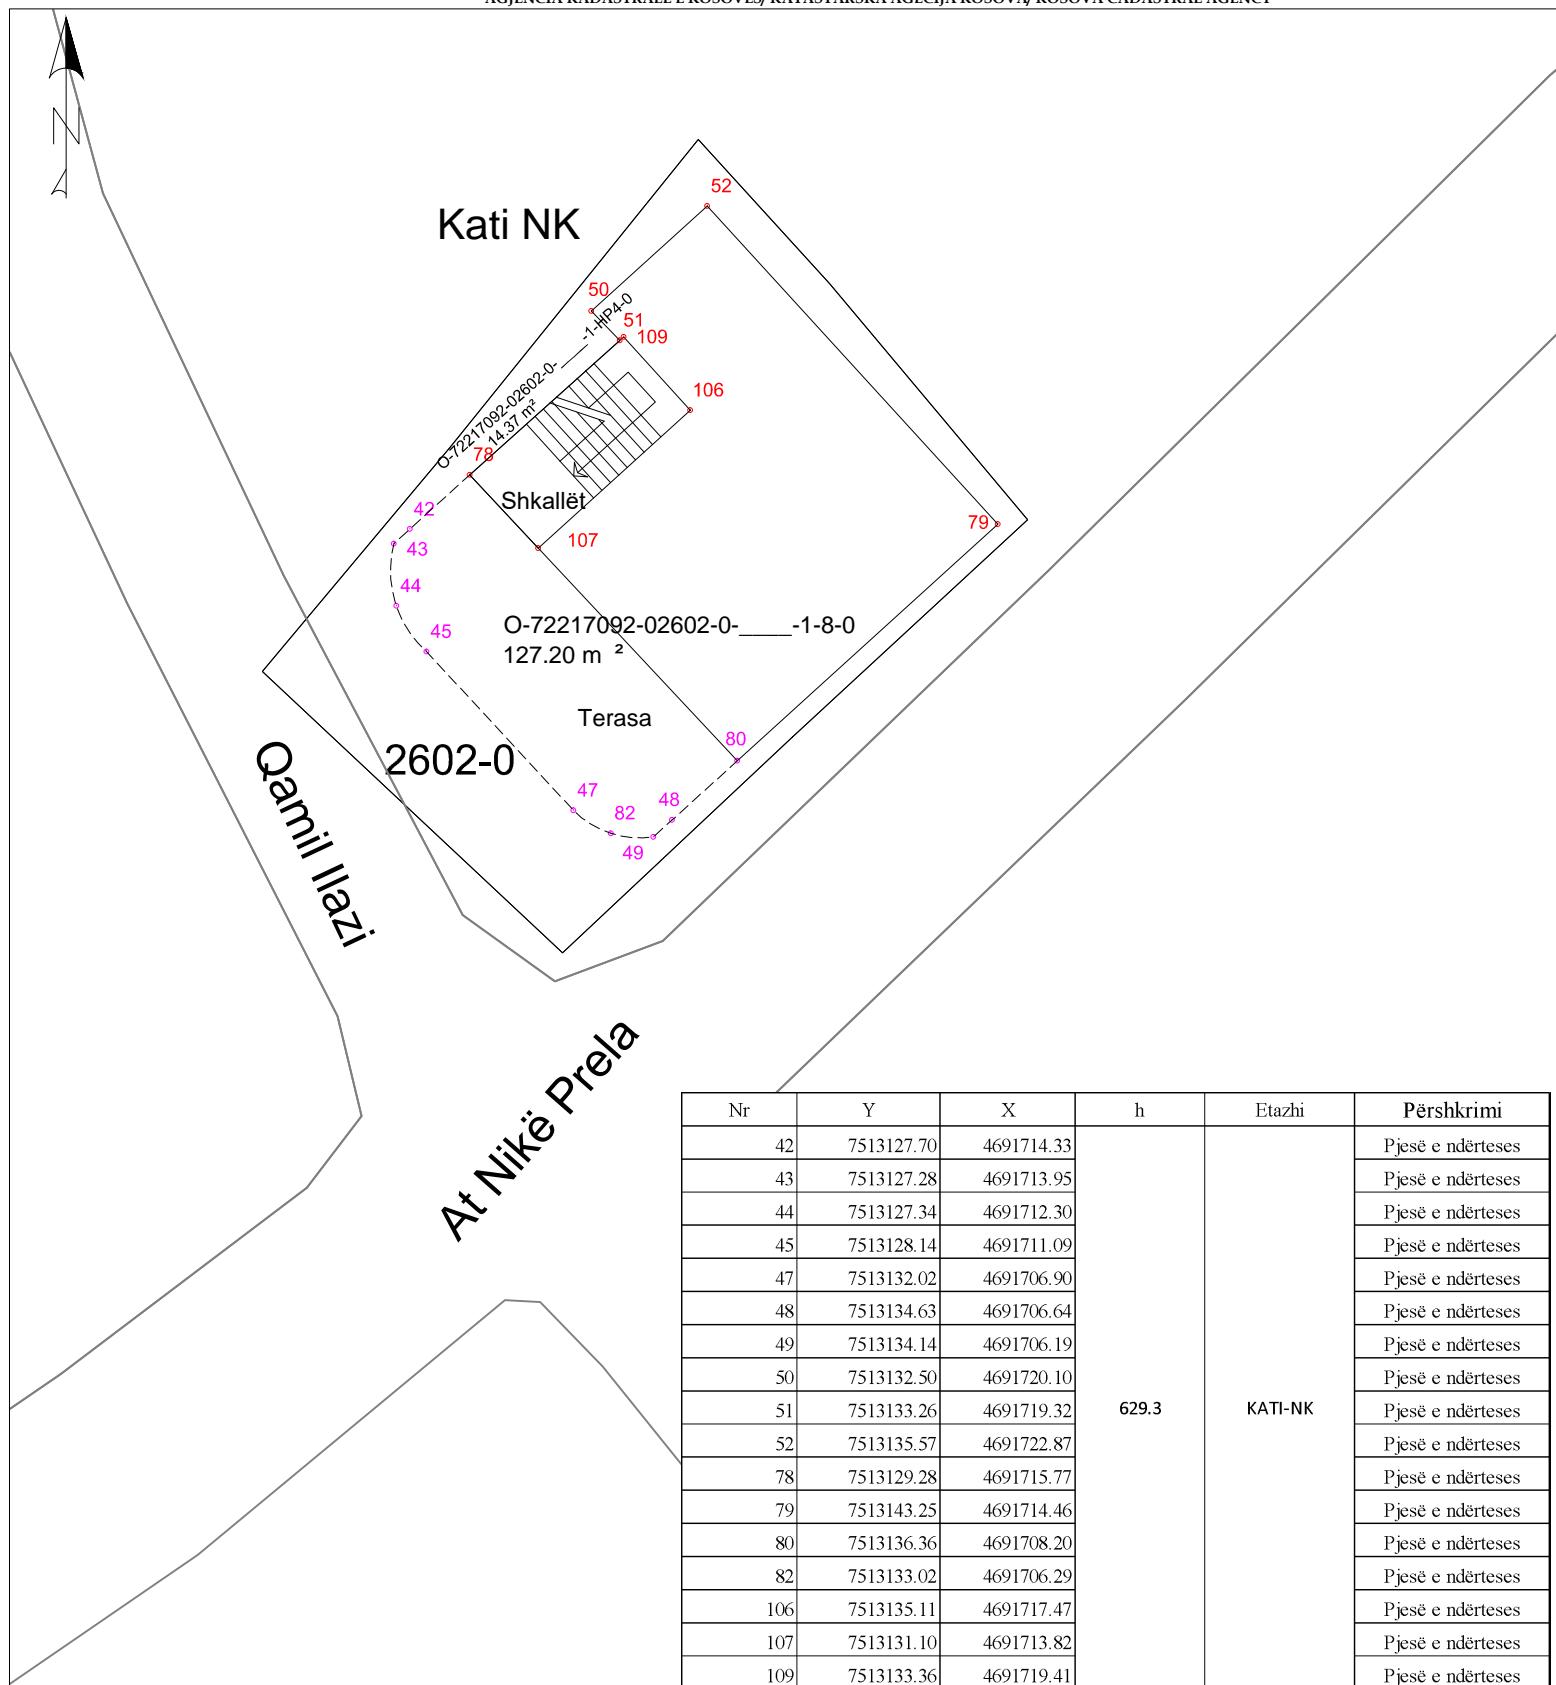Rilevoi / Snimio: LIRIDON SEJDIU
(emri dhe mbiemri i gjyqetarit/kompanisë/ ime i prezime geodeta/ kompanije)Aprovoi / Usvojio: _____
(emri dhe mbiemri i përsorit zyrtar/ ime i prezime sluzbeneg lica)Nr. i licencës / Br. licence: 140

V.V.

Nënshkrimi / Potpis: _____

Nënshkrimi / Potpis: _____

Data e rilevimit / Datum snimanja: 12.04.2021

Data e rilevimit / Datum snimanja: _____



Republika e Kosovës
Republika Kosova-Republic of Kosovo
Qeveria e Kosovës- Vlada Kosova- Government of Kosovo
Ministria e Infrastrukturës dhe Ambientit/ Ministrastvo Infrastrukture i Sredine/ Ministry of Infrastructure and Environment
AGJENCIA KADASTRALE E KOSOVËS/KOSOVSKA KATASTARSKA AGENCIJA/ KOSOVO CADASTRAL AGENCY

Komuna: Ferizaj

Numri i njësisë kadastrale: 02602-0

Zona Kadastrale: Ferizaj

Sistemi koordinat: KosovaRef01

| Nr | Y | X | H | Kodi | Përshkrimi | Burimi |
|----|-------------|-------------|---------|------|-----------------|--------|
| 1 | 7513135.568 | 4691722.874 | 620.112 | 40 | Shtëpi-Ndërtesë | PM |
| 2 | 7513132.501 | 4691720.099 | 620.112 | 40 | Shtëpi-Ndërtesë | PM |
| 6 | 7513133.257 | 4691719.323 | 620.112 | 40 | Shtëpi-Ndërtesë | PM |
| 7 | 7513128.986 | 4691715.505 | 620.112 | 40 | Shtëpi-Ndërtesë | PM |
| 11 | 7513130.596 | 4691713.706 | 620.112 | 40 | Shtëpi-Ndërtesë | PM |
| 12 | 7513129.454 | 4691712.656 | 620.112 | 40 | Shtëpi-Ndërtesë | PM |
| 13 | 7513129.172 | 4691712.005 | 620.112 | 40 | Shtëpi-Ndërtesë | PM |
| 14 | 7513129.620 | 4691710.995 | 620.112 | 40 | Shtëpi-Ndërtesë | PM |
| 15 | 7513132.685 | 4691707.655 | 620.112 | 40 | Shtëpi-Ndërtesë | PM |
| 65 | 7513134.155 | 4691707.022 | 620.112 | 40 | Shtëpi-Ndërtesë | PM |
| 67 | 7513135.857 | 4691707.745 | 620.112 | 40 | Shtëpi-Ndërtesë | PM |
| 68 | 7513143.253 | 4691714.464 | 620.112 | 40 | Shtëpi-Ndërtesë | PM |
| 8 | 7513128.764 | 4691715.831 | 620.112 | 40 | Shtëpi-Ndërtesë | PM |
| 9 | 7513126.840 | 4691714.119 | 620.112 | 40 | Shtëpi-Ndërtesë | PM |
| 10 | 7513129.257 | 4691711.459 | 620.112 | 40 | Shtëpi-Ndërtesë | PM |
| 98 | 7513129.791 | 4691714.606 | 620.112 | 40 | Shtëpi-Ndërtesë | PM |
| 98 | 7513129.791 | 4691714.606 | 620.112 | - | Hyreje | PM |

| Nr | Y | X | h | Etazhi | Përshkrimi |
|-----|------------|------------|---|--------|-------------------|
| 1 | 7513135.57 | 4691722.87 | | | Pjesë e ndërteses |
| 2 | 7513132.50 | 4691720.10 | | | Pjesë e ndërteses |
| 6 | 7513133.26 | 4691719.32 | | | Pjesë e ndërteses |
| 7 | 7513128.99 | 4691715.51 | | | Pjesë e ndërteses |
| 11 | 7513130.60 | 4691713.71 | | | Pjesë e ndërteses |
| 12 | 7513129.45 | 4691712.66 | | | Pjesë e ndërteses |
| 13 | 7513129.17 | 4691712.01 | | | Pjesë e ndërteses |
| 14 | 7513129.62 | 4691711.00 | | | Pjesë e ndërteses |
| 15 | 7513132.69 | 4691707.66 | | | Pjesë e ndërteses |
| 65 | 7513134.16 | 4691707.02 | | | Pjesë e ndërteses |
| 67 | 7513135.86 | 4691707.75 | | | Pjesë e ndërteses |
| 68 | 7513143.25 | 4691714.46 | | | Pjesë e ndërteses |
| 101 | 7513138.23 | 4691719.96 | | | Pjesë e ndërteses |
| 102 | 7513134.83 | 4691717.63 | | | Pjesë e ndërteses |
| 103 | 7513135.25 | 4691717.19 | | | Pjesë e ndërteses |
| 104 | 7513131.21 | 4691717.49 | | | Pjesë e ndërteses |
| 8 | 7513128.76 | 4691715.83 | | | Pjesë e ndërteses |
| 9 | 7513126.84 | 4691714.12 | | | Pjesë e ndërteses |
| 10 | 7513129.26 | 4691711.46 | | | Pjesë e ndërteses |

Koordinatat janë gjeneruar pas pozicionimit të pjesëve të ndertesës në sistem koordinat Kosovaref01

| | | |
|---|----------------|----------------------|
| Gjeodeti / Kompania gjeodete e licencuar: | Liridon Sejdiu | Nënshkrimi dhe vula: |
| Numri i licencës | 140 | |



Republika e Kosovës

Republika Kosova-Republic of Kosovo

Geveria e Kosovës- Vlada Kosova- Government of Kosovo

Ministria e Infrastrukturës dhe Ambientit/ Ministrastvo Infrastrukture i Sredine/ Ministry of Infrastructure and Environment

AGJENCIJA KADASTRALE E KOSOVËS/KOSOVSKA KATASTARSKA AGENCIJA/ KOSOVO CADASTRAL AGENCY

| Komuna: Ferizaj | | | Zona Kadastrale: Ferizaj | | | |
|---|------------|------------|--------------------------------|---------|--------------------|--|
| Numri i njësisë kadastrale: 02602-0 | | | Sistemi koordinat: KosovaRef01 | | | |
| Nr | Y | X | h | Etazhi | Përshkrimi | |
| 1 | 7513135.57 | 4691722.87 | 623.174 | KATI1 | Pjesë e ndërtueses | |
| 2 | 7513132.50 | 4691720.10 | | | Pjesë e ndërtueses | |
| 7 | 7513128.99 | 4691715.51 | | | Pjesë e ndërtueses | |
| 23 | 7513133.25 | 4691719.32 | | | Pjesë e ndërtueses | |
| 24 | 7513127.28 | 4691713.95 | | | Pjesë e ndërtueses | |
| 25 | 7513127.38 | 4691712.19 | | | Pjesë e ndërtueses | |
| 26 | 7513128.14 | 4691711.09 | | | Pjesë e ndërtueses | |
| 27 | 7513132.02 | 4691706.90 | | | Pjesë e ndërtueses | |
| 28 | 7513133.52 | 4691706.18 | | | Pjesë e ndërtueses | |
| 65 | 7513134.14 | 4691706.19 | | | Pjesë e ndërtueses | |
| 67 | 7513135.86 | 4691707.75 | | | Pjesë e ndërtueses | |
| 68 | 7513143.25 | 4691714.46 | | | Pjesë e ndërtueses | |
| 106 | 7513135.00 | 4691717.37 | | | Pjesë e ndërtueses | |
| 107 | 7513131.30 | 4691714.01 | | | Pjesë e ndërtueses | |
| 108 | 7513129.53 | 4691715.99 | | | Pjesë e ndërtueses | |
| 109 | 7513131.21 | 4691714.11 | | | Pjesë e ndërtueses | |
| 110 | 7513128.01 | 4691711.22 | | | Pjesë e ndërtueses | |
| Nr | Y | X | h | Etazhi | Përshkrimi | |
| 1 | 7513135.57 | 4691722.87 | 626.094 | KATI2 | Pjesë e ndërtueses | |
| 2 | 7513132.50 | 4691720.10 | | | Pjesë e ndërtueses | |
| 7 | 7513128.99 | 4691715.51 | | | Pjesë e ndërtueses | |
| 23 | 7513133.25 | 4691719.32 | | | Pjesë e ndërtueses | |
| 24 | 7513127.28 | 4691713.95 | | | Pjesë e ndërtueses | |
| 25 | 7513127.38 | 4691712.19 | | | Pjesë e ndërtueses | |
| 26 | 7513128.14 | 4691711.09 | | | Pjesë e ndërtueses | |
| 27 | 7513132.02 | 4691706.90 | | | Pjesë e ndërtueses | |
| 28 | 7513133.52 | 4691706.18 | | | Pjesë e ndërtueses | |
| 65 | 7513134.14 | 4691706.19 | | | Pjesë e ndërtueses | |
| 67 | 7513135.86 | 4691707.75 | | | Pjesë e ndërtueses | |
| 68 | 7513143.25 | 4691714.46 | | | Pjesë e ndërtueses | |
| 106 | 7513135.00 | 4691717.37 | | | Pjesë e ndërtueses | |
| 107 | 7513131.30 | 4691714.01 | | | Pjesë e ndërtueses | |
| 108 | 7513129.53 | 4691715.99 | | | Pjesë e ndërtueses | |
| 109 | 7513131.21 | 4691714.11 | | | Pjesë e ndërtueses | |
| 110 | 7513128.01 | 4691711.22 | | | Pjesë e ndërtueses | |
| Nr | Y | X | h | Etazhi | Përshkrimi | |
| 42 | 7513127.70 | 4691714.33 | 629.3 | KATI-NK | Pjesë e ndërtueses | |
| 43 | 7513127.28 | 4691713.95 | | | Pjesë e ndërtueses | |
| 44 | 7513127.34 | 4691712.30 | | | Pjesë e ndërtueses | |
| 45 | 7513128.14 | 4691711.09 | | | Pjesë e ndërtueses | |
| 47 | 7513132.02 | 4691706.90 | | | Pjesë e ndërtueses | |
| 48 | 7513134.63 | 4691706.64 | | | Pjesë e ndërtueses | |
| 49 | 7513134.14 | 4691706.19 | | | Pjesë e ndërtueses | |
| 50 | 7513132.50 | 4691720.10 | | | Pjesë e ndërtueses | |
| 51 | 7513133.26 | 4691719.32 | | | Pjesë e ndërtueses | |
| 52 | 7513135.57 | 4691722.87 | | | Pjesë e ndërtueses | |
| 78 | 7513129.28 | 4691715.77 | | | Pjesë e ndërtueses | |
| 79 | 7513143.25 | 4691714.46 | | | Pjesë e ndërtueses | |
| 80 | 7513136.36 | 4691708.20 | | | Pjesë e ndërtueses | |
| 82 | 7513133.02 | 4691706.29 | | | Pjesë e ndërtueses | |
| 106 | 7513135.11 | 4691717.47 | | | Pjesë e ndërtueses | |
| 107 | 7513131.10 | 4691713.82 | | | Pjesë e ndërtueses | |
| 109 | 7513133.36 | 4691719.41 | | | Pjesë e ndërtueses | |
| Gjeodeti / Kompania gjeodete e licencuar: | | | Liridon Sejdiu | | | |
| Numri i licencës | | | 140 | | | |
| | | | Nënshkrimi dhe vula: | | | |



Republika e Kosovës

Republika Kosova-Republic of Kosovo

Qeveria -Vlada-Government

Ministria e Infrastrukturës dhe Ambientit / Ministarstvo Infrastrukture i Sredine / Ministry of Infrastructure and Environment

AGENCIJA KADASTRALE E KOSOVËS/ KATASTARSKA AGENCIJA KOSOVA/ KOSOVA CADASTRAL AGENCY

REGJISTRI I PJESËVE TË NDËRTESËS

Gjeodeti apo kompania gjeodete e licencuar: LIRIDON SEJDIU numri i licencës: 140

| Nr | Komuna | Zona Kadastrale | Numri i ndërtesës | Sipërfaqja [m ²] | Lloji i Ndërtesës | Adresa e Ndërtesës | Vendi i quajtur | Leja e ndertimit | Pronari / Shfrytëzuesi | Numri personal | Adresa e pronarit | Pjesa e Pronësisë |
|----|---------|-----------------|-------------------------|------------------------------|-------------------|---------------------------|-----------------|------------------|-------------------------|----------------|-------------------|-------------------|
| 1 | Ferizaj | Ferizaj | O-72217092-02602-0-____ | 125.20 | Ndërtesë | Rr. " AT NIKPRELAJ" nr 47 | AT NIKPRELAJ | JO | Albnor (Gazemend) Shehu | 123339128 | Doganaj-Kaçanik | 1/1 |

N D E R T E S A O-72217092-02602-0-













