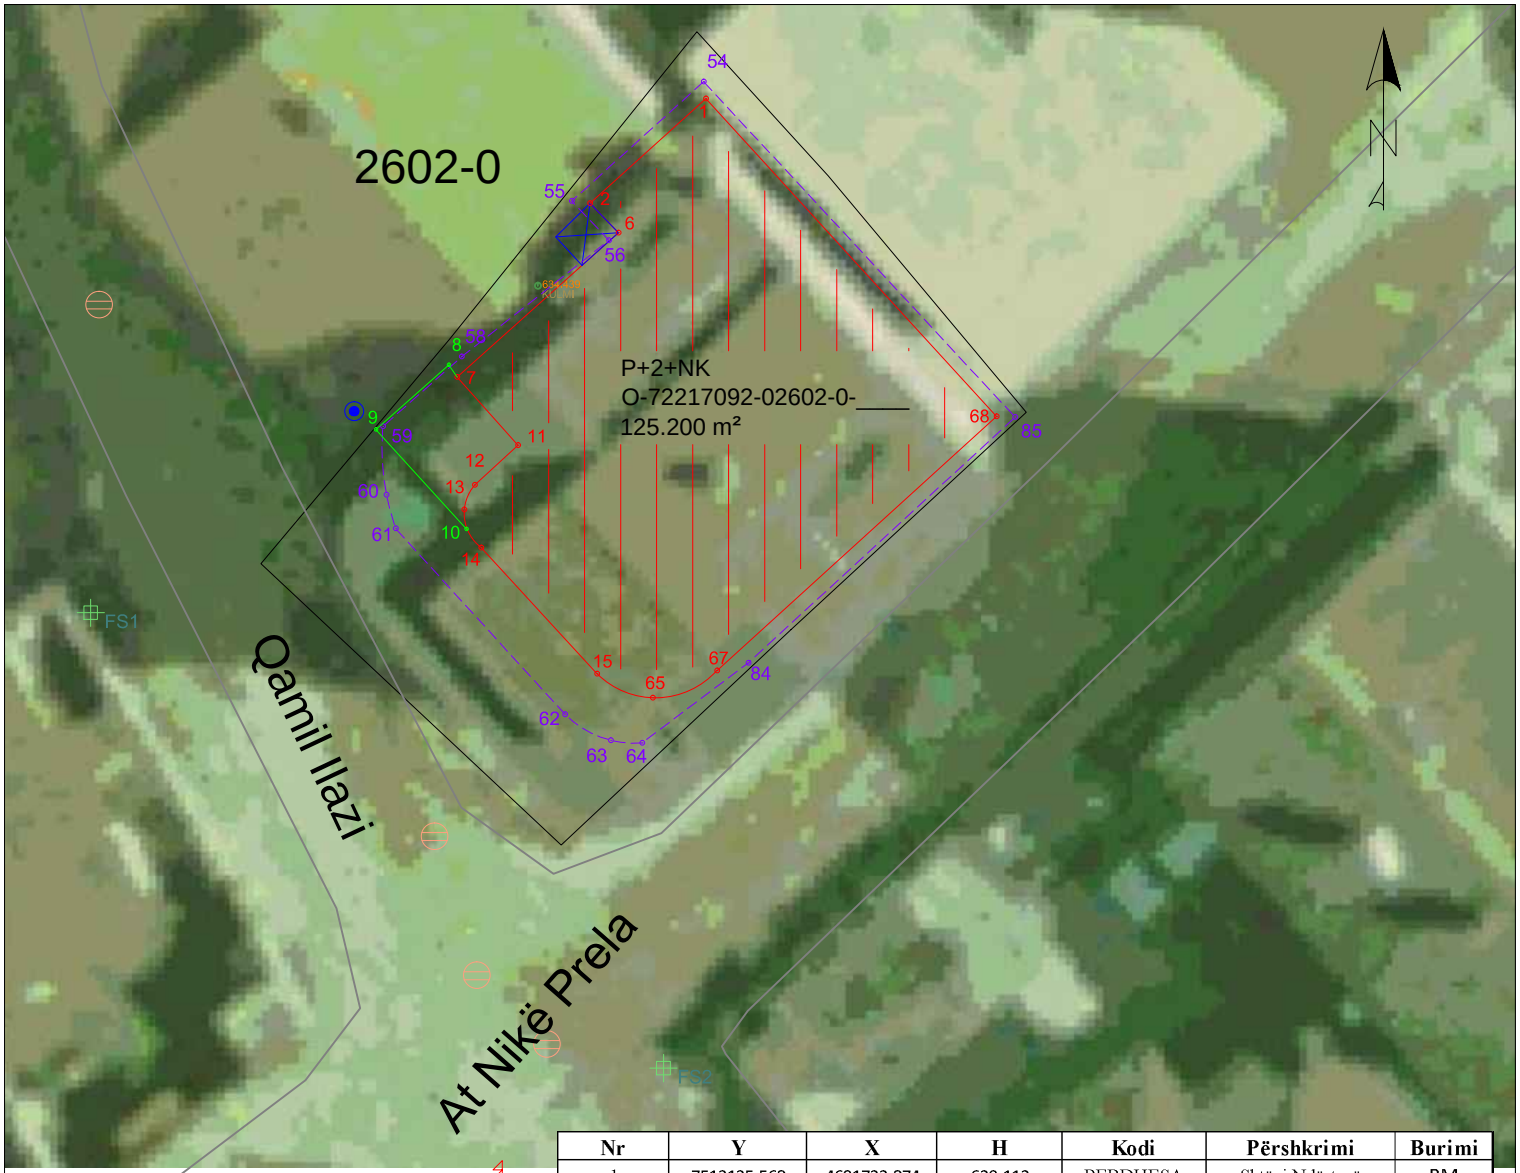

Nr	Y	X	H	Kodi	Përshkrimi	Burimi
1	7513135.568	4691722.874	620.112	PERDHESA	Shtëpi-Ndërtesë	PM
2	7513132.501	4691720.099	620.112	PERDHESA	Shtëpi-Ndërtesë	PM
6	7513133.257	4691719.323	620.112	PERDHESA	Shtëpi-Ndërtesë	PM
7	7513128.986	4691715.505	620.112	PERDHESA	Shtëpi-Ndërtesë	PM
11	7513130.596	4691713.706	620.112	PERDHESA	Shtëpi-Ndërtesë	PM
12	7513129.454	4691712.656	620.112	PERDHESA	Shtëpi-Ndërtesë	PM
13	7513129.172	4691712.005	620.112	PERDHESA	Shtëpi-Ndërtesë	PM
14	7513129.620	4691710.995	620.112	PERDHESA	Shtëpi-Ndërtesë	PM
15	7513132.685	4691707.655	620.112	PERDHESA	Shtëpi-Ndërtesë	PM
65	7513134.155	4691707.022	620.112	PERDHESA	Shtëpi-Ndërtesë	PM
67	7513135.857	4691707.745	620.112	PERDHESA	Shtëpi-Ndërtesë	PM
68	7513143.253	4691714.464	620.112	PERDHESA	Shtëpi-Ndërtesë	PM

Republika e Kosovës

Qeveria -Vlada

Ministria e Mjedisit dhe Planifikimit Hapësinr /Ministarstv Sredine i Prstrng Planiranja

AGJENCIA KADASTRALE E KOSOVËS/ KATASTARSKA AGENCIJA KOSOVA

Situacioni i terrenit

Orto 2004

Zyra kadastrale kmunale / pštinska katastarska kancelarija: Ferizaj

Zona kadastrale / Katastarska zona: Ferizaj

Nr. i njësisë kadastrale / Br. katastarske jedinice : 2602-0

Numri i lëndës / Broj predmeta: _____

Shkalla e zvoglimit / Razmera plana 1: 200

Lista e koordinatave të pikave të matura:

Nr	Y	X	H	DSC
88	7513119.293	4691709.275	619.928	FS1
92	7513134.444	4691697.230	619.819	FS2
53	7513131.118	4691717.922	634.439	KULMI
17	7513126.261	4691714.600	620.056	KYQJE-UJSJELLES
1	7513135.568	4691722.874	620.112	PERDHESA
2	7513132.501	4691720.099	620.112	PERDHESA
6	7513133.257	4691719.323	620.112	PERDHESA
7	7513128.986	4691715.505	620.112	PERDHESA
11	7513130.596	4691713.706	620.112	PERDHESA
12	7513129.454	4691712.656	620.112	PERDHESA
13	7513129.172	4691712.005	620.112	PERDHESA
14	7513129.620	4691710.995	620.112	PERDHESA
15	7513132.685	4691707.655	620.112	PERDHESA
65	7513134.155	4691707.022	620.112	PERDHESA
67	7513135.857	4691707.745	620.112	PERDHESA
68	7513143.253	4691714.464	620.112	PERDHESA
18	7513119.512	4691717.419	619.807	PUSET-FEKAL
19	7513128.384	4691703.361	619.737	PUSET-FEKAL
20	7513129.499	4691699.684	619.688	PUSET-FEKAL
21	7513131.355	4691697.861	619.721	PUSET-FEKAL

Nr	Y	X	H	DSC
8	7513128.764	4691715.831	620.112	SHKALET
9	7513126.840	4691714.119	620.112	SHKALET
10	7513129.231	4691711.487	620.112	SHKALET
22	7513130.176	4691693.961	619.757	SHTYLL-ELEKTRIKE
86	7513106.321	4691683.375	619.497	ST1
87	7513162.150	4691668.332	619.825	ST2
54	7513135.505	4691723.319	631.507	STREHA
55	7513132.018	4691720.161	631.507	STREHA
56	7513133.002	4691719.123	631.507	STREHA
57	7513132.790	4691719.412	631.507	STREHA
58	7513129.105	4691716.044	631.507	STREHA
59	7513127.020	4691714.199	631.507	STREHA
60	7513127.147	4691713.062	631.507	STREHA
61	7513127.359	4691711.499	631.507	STREHA
62	7513131.843	4691706.582	631.507	STREHA
63	7513133.047	4691705.902	631.507	STREHA
64	7513133.876	4691705.829	631.507	STREHA
84	7513136.690	4691707.949	631.507	STREHA
85	7513143.745	4691714.446	631.507	STREHA

Shpjegues:

- Kufiri kadastral (nga SIKTK-G)
- Ndërtesa në trajtim për legalizim
- Ndërtesa tjera
- Aneks Ndërtimi
- Shtyllë elektrike
- Pusetë e ujësjellësit
- Pusetë e ujërave të zeza
- Strehët
- Shkallët
- 91 Pikë e objekteve fqinje
- Rr. Emri i rrugës
- P4 Pikë e rrjetës gjeodezike
- 131 Pikë e strehëve
- 81 Pikë e terasës
- 10 Pikë e objektit
- 93 Pikë e murit
- 92 Pikë e kulmit
- Bunari

Rilevoi / Snimi: LIRIDON SEJDIU

(emri dhe mbiemri i gjedetit/kompanisë/ ime i prezime gedeta/ kompanije)

Nr. i licencës / Br. licence: 140

Data e rilevimit / Datum snimanja: 12.04.2021

Nënshkrimi / Potpis: _____

V.V.