Zyra kadastrale komunale / Opštinska katastarska kancelarija: Ferizaj

Zona kadastrale / Katastarska zona: Ferizaj

Lloji i njësisë kadastrale / Vrsta katastarske jedinice : Pjesë e ndërtesës

Nr. i njësisë kadastrale / Br. katastarske jedinice : 2602-0

Numri i lëndës / Broj predmeta:

Shkalla e zvoglimit / Razmera plana 1: 200

Republika e Kosovës

Republika Kosova-Republic of Kosova

Qeveria -Vlada-Government

Ministria e Mjedisit dhe Planifikimit Hapësinor /Ministarstvo Sredine i Prostornog Planiranja/Ministry of Environment and Spatial Planning

AGJENCIA KADASTRALE E KOSOVËS/ KATASTARSKA AGECIJA KOSOVA/ KOSOVA CADASTRAL AGENCY

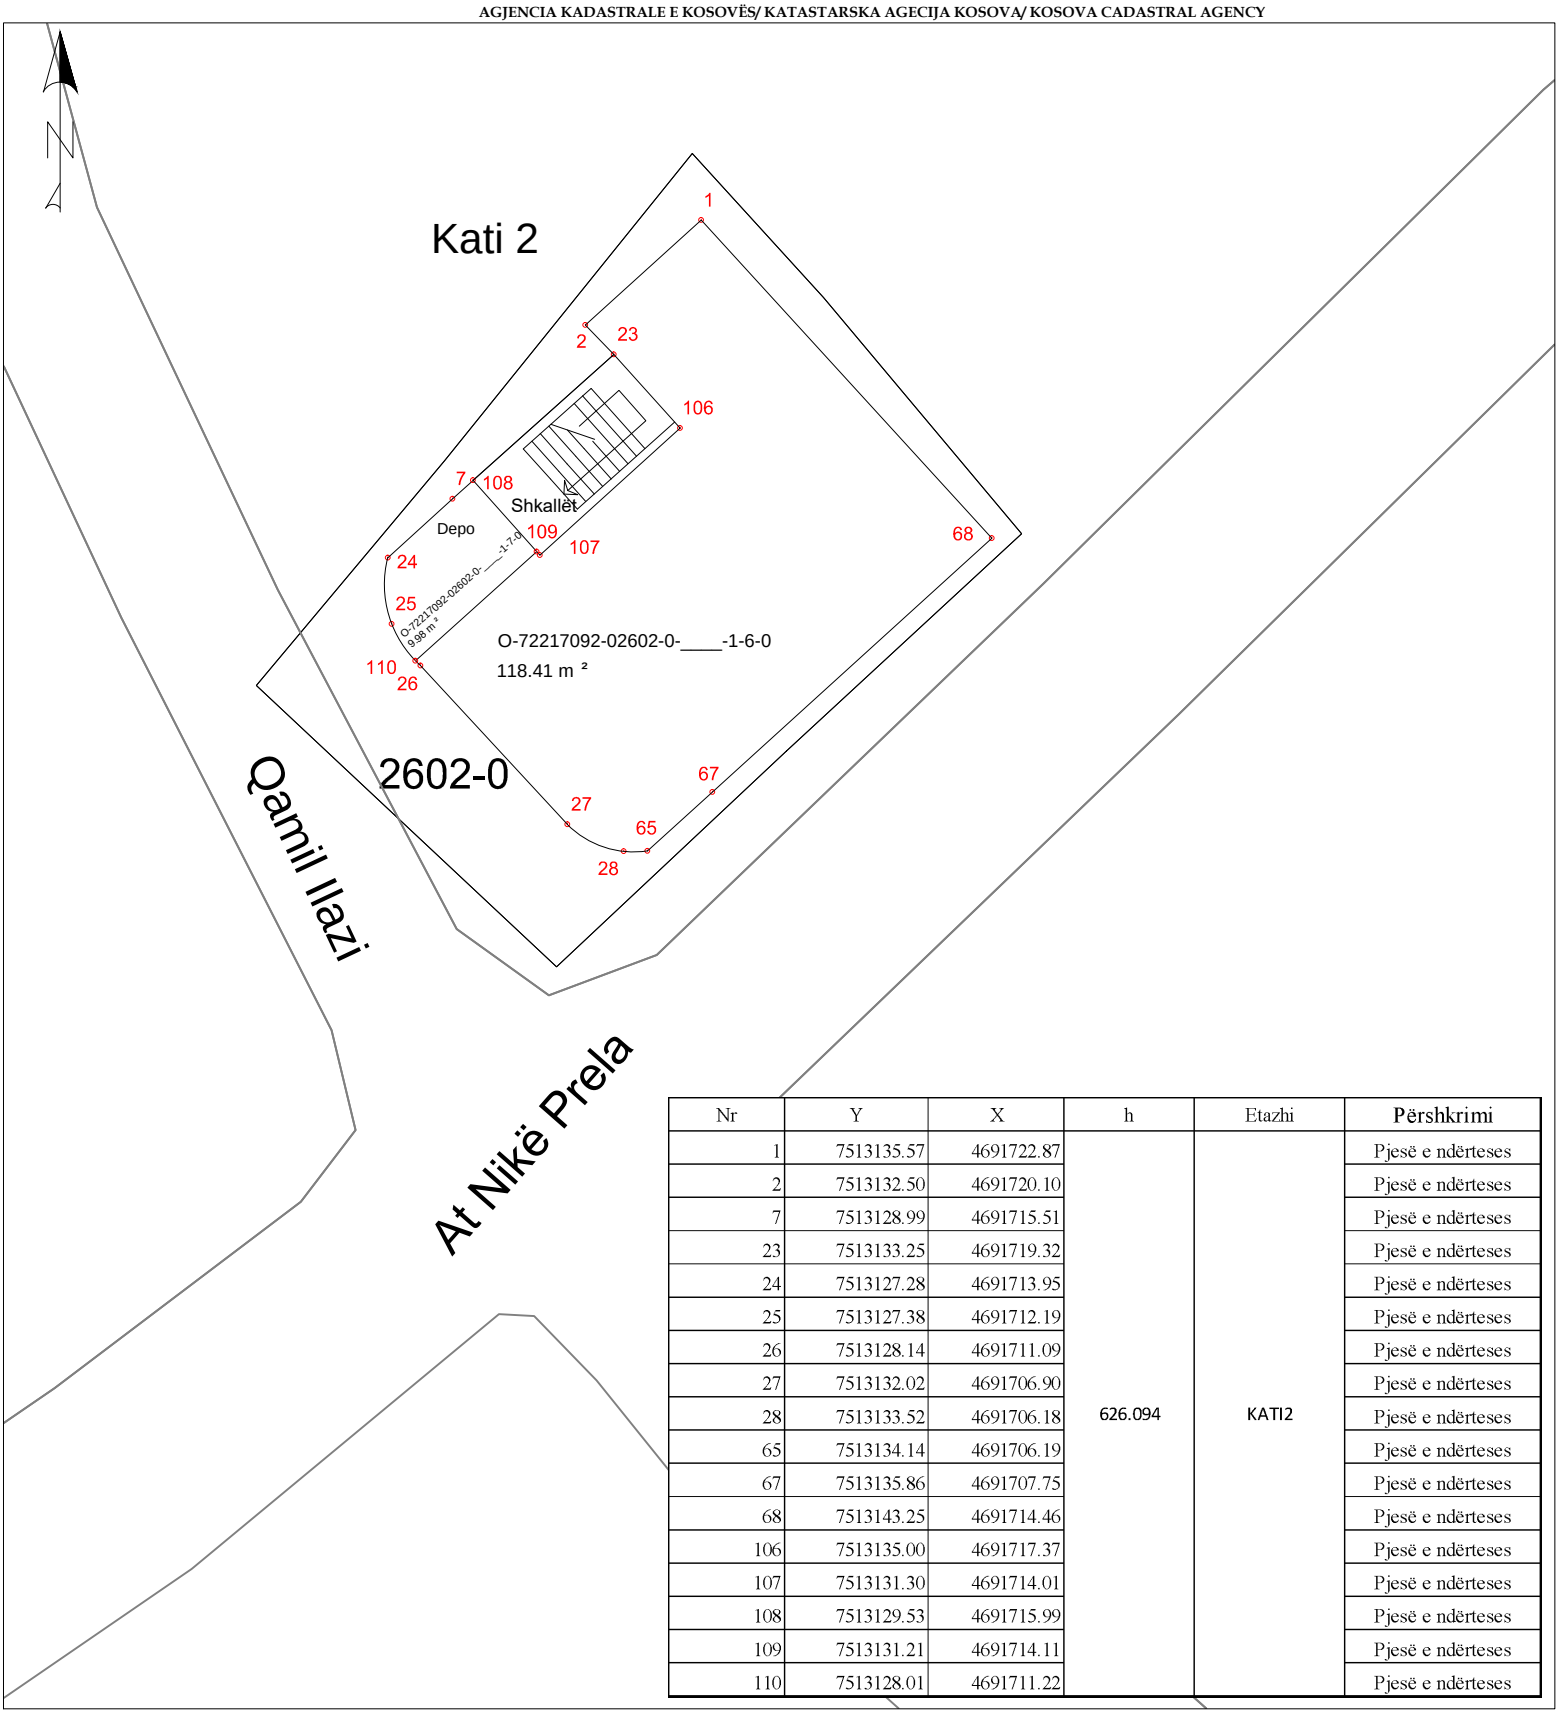

Nr	Y	X	h	Etazhi	Përshkrimi
1	7513135.57	4691722.87	626.094	KATI2	Pjesë e ndërteses
2	7513132.50	4691720.10			Pjesë e ndërteses
7	7513128.99	4691715.51			Pjesë e ndërteses
23	7513133.25	4691719.32			Pjesë e ndërteses
24	7513127.28	4691713.95			Pjesë e ndërteses
25	7513127.38	4691712.19			Pjesë e ndërteses
26	7513128.14	4691711.09			Pjesë e ndërteses
27	7513132.02	4691706.90			Pjesë e ndërteses
28	7513133.52	4691706.18			Pjesë e ndërteses
65	7513134.14	4691706.19			Pjesë e ndërteses
67	7513135.86	4691707.75			Pjesë e ndërteses
68	7513143.25	4691714.46			Pjesë e ndërteses
106	7513135.00	4691717.37			Pjesë e ndërteses
107	7513131.30	4691714.01			Pjesë e ndërteses
108	7513129.53	4691715.99			Pjesë e ndërteses
109	7513131.21	4691714.11			Pjesë e ndërteses
110	7513128.01	4691711.22			Pjesë e ndërteses

Rilevoi / Snimio: SEAD PRUSHI
(emri dhe mbiemri i gjeodetit/kompanisë/ ime i prezime geodeta/ kompanije)

Nr. i licencës / Br. licence: 152

Nënshkrimi / Potpis:

Data e rilevimit / Datum snimanja: 10.10.2020

V.V.

Aprovoi / Usvojio:
(emri dhe mbiemri i përsonit zyrtar/ ime i prezime sluzbenog lica)

Nënshkrimi / Potpis:

Data e rilevimit / Datum snimanja: