Zyra kadastrale komunale / Opštinska katastarska kancelarija: Ferizaj

Nr. i njësisë kadastrale / Br. katastarske jedinice : 2602-0

Zona kadastrale / Katastarska zona: Ferizaj

Numri i lëndës / Broj predmeta:

Lloji i njësisë kadastrale / Vrsta katastarske jedinice : Ndërtesë

Shkalla e zvoglimit / Razmera plana 1: 200

Republika e Kosovës

Republika Kosova-Republic of Kosova

Qeveria -Vlada-Government

Ministria e Mjedisit dhe Planifikimit Hapësinor /Ministarstvo Sredine i Prostornog Planiranja/Ministry of Environment and Spatial Planning

AGJENCIA KADASTRALE E KOSOVËS/ KATASTARSKA AGECIJA KOSOVA/ KOSOVA CADASTRAL AGENCY

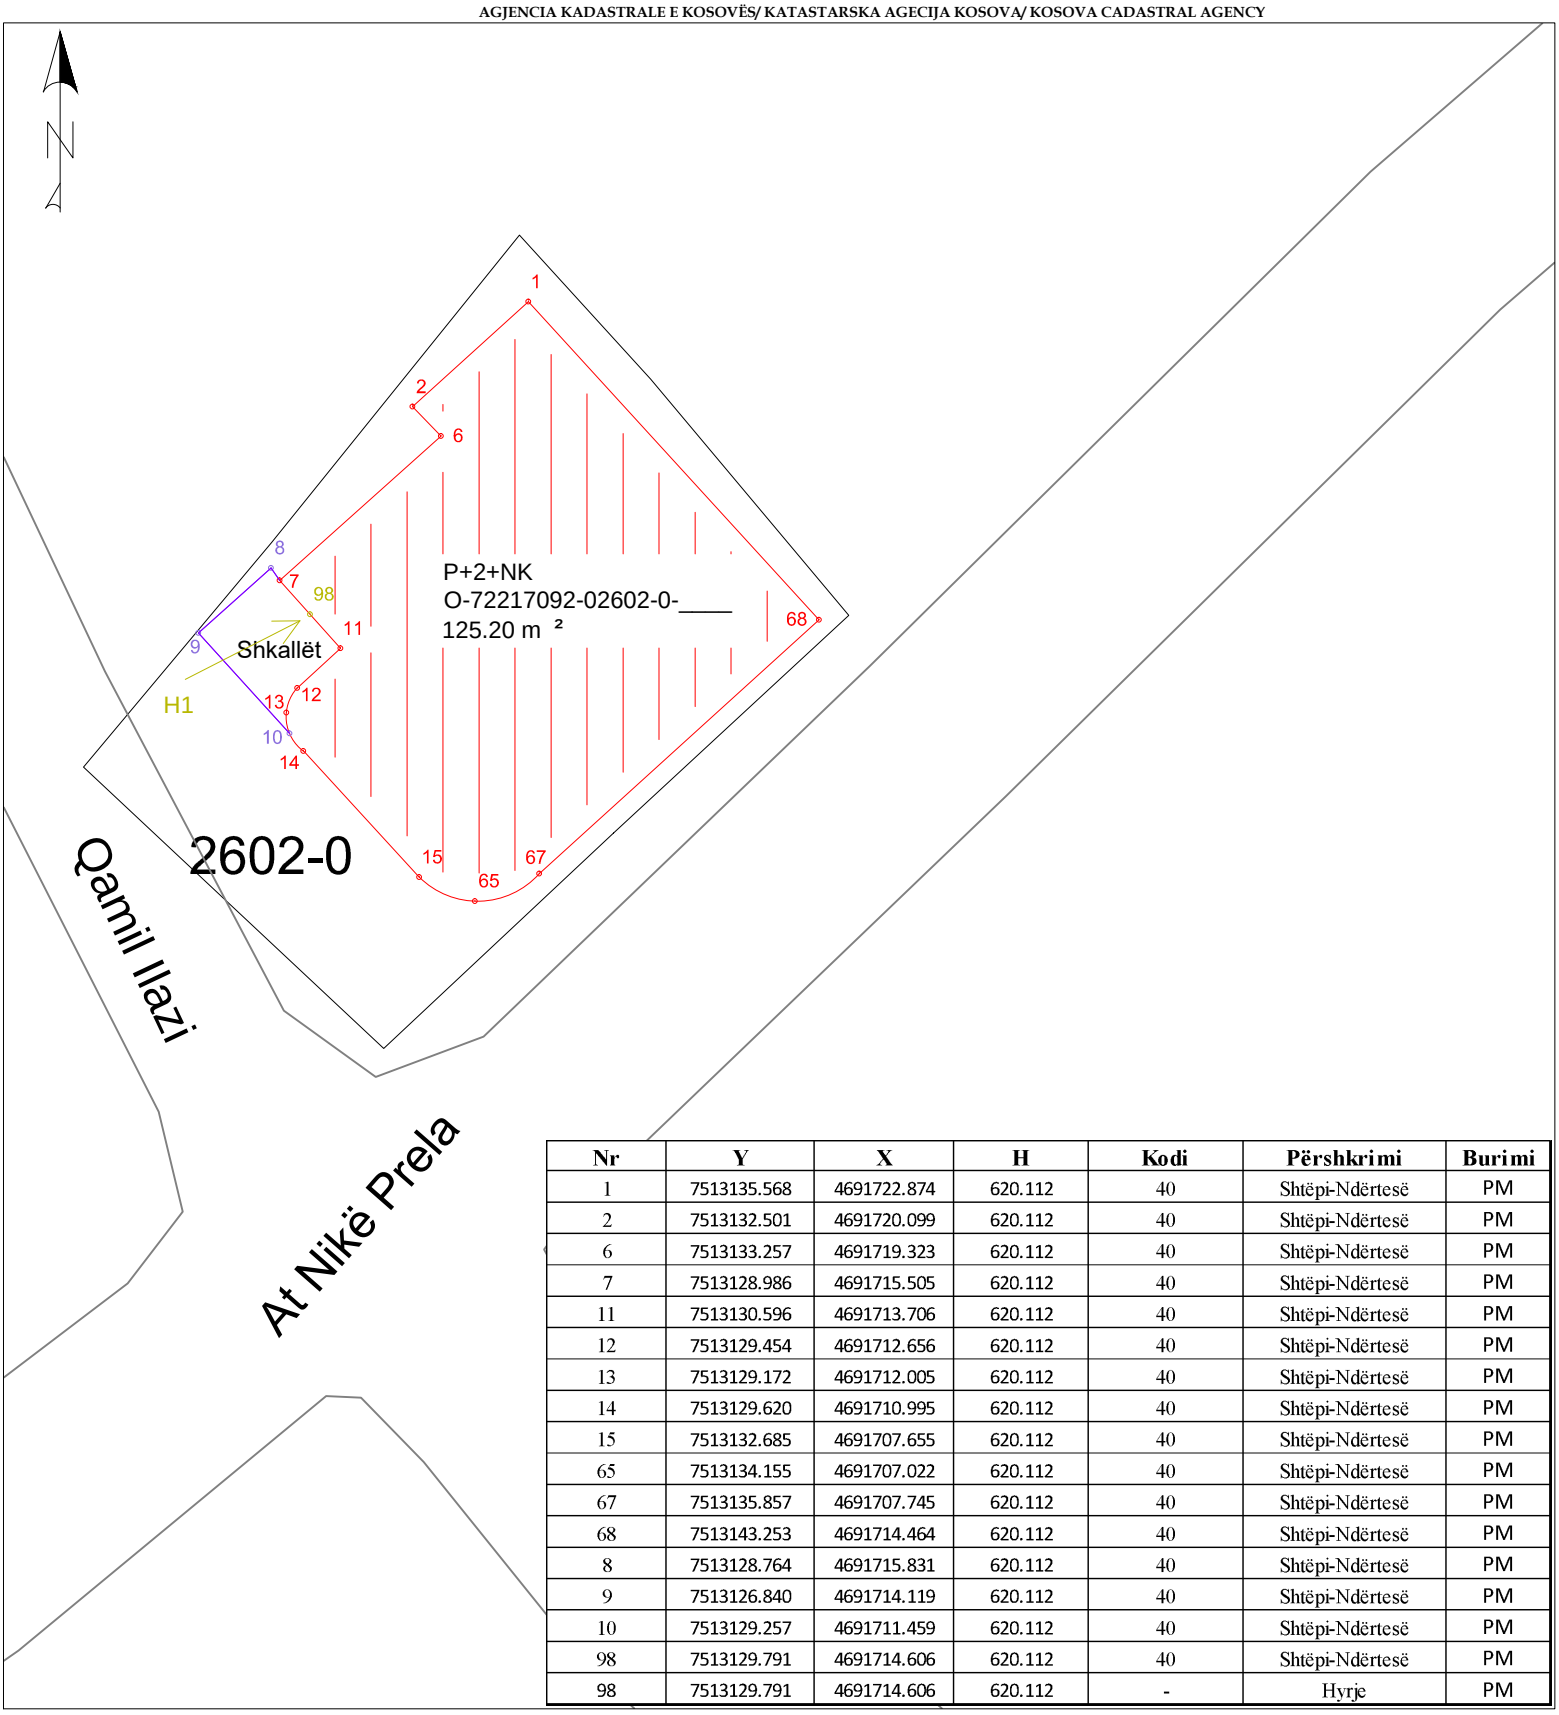

Nr	Y	X	H	Kodi	Përshkrimi	Burimi
1	7513135.568	4691722.874	620.112	40	Shtëpi-Ndërtesë	PM
2	7513132.501	4691720.099	620.112	40	Shtëpi-Ndërtesë	PM
6	7513133.257	4691719.323	620.112	40	Shtëpi-Ndërtesë	PM
7	7513128.986	4691715.505	620.112	40	Shtëpi-Ndërtesë	PM
11	7513130.596	4691713.706	620.112	40	Shtëpi-Ndërtesë	PM
12	7513129.454	4691712.656	620.112	40	Shtëpi-Ndërtesë	PM
13	7513129.172	4691712.005	620.112	40	Shtëpi-Ndërtesë	PM
14	7513129.620	4691710.995	620.112	40	Shtëpi-Ndërtesë	PM
15	7513132.685	4691707.655	620.112	40	Shtëpi-Ndërtesë	PM
65	7513134.155	4691707.022	620.112	40	Shtëpi-Ndërtesë	PM
67	7513135.857	4691707.745	620.112	40	Shtëpi-Ndërtesë	PM
68	7513143.253	4691714.464	620.112	40	Shtëpi-Ndërtesë	PM
8	7513128.764	4691715.831	620.112	40	Shtëpi-Ndërtesë	PM
9	7513126.840	4691714.119	620.112	40	Shtëpi-Ndërtesë	PM
10	7513129.257	4691711.459	620.112	40	Shtëpi-Ndërtesë	PM
98	7513129.791	4691714.606	620.112	40	Shtëpi-Ndërtesë	PM
98	7513129.791	4691714.606	620.112	-	Hyrje	PM

Rilevoi / Snimio: LIRIDON SEJDIU

(emri dhe mbiemri i gjeodetit/kompanisë/ ime i prezime geodeta/ kompanije)

Nr. i licencës / Br. licence: 140

Nënshkrimi / Potpis:

Data e rilevimit / Datum snimanja: 12.04.2021

V.V.

Aprovoi / Usvojio:

(emri dhe mbiemri i përsonit zyrtar/ ime i prezime sluzbenog lica)

Nënshkrimi / Potpis:

Data e rilevimit / Datum snimanja: